
ONSITE / HERON REACH

A coordinated build brief for Claude / original ONSITE geometry / 32-player design target

B000 / ISSUE INDEX

READ THIS ISSUE BEFORE MODELLING

All floor plans use the same surveyed-style site origin and level datums.

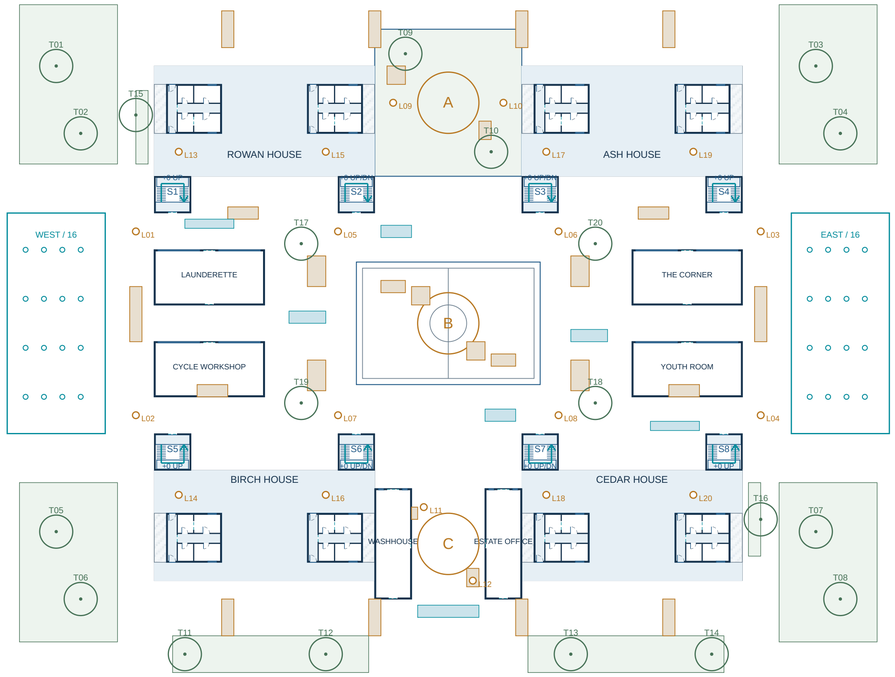

1:500 AT A1 / METRES

0 20 40 m

SHEET	TITLE	SCALE
B100	Site setting-out / coordinate schedule	1:250
B101	Ground floor / homes and shop portals	1:250
B102	Gallery level +3.00	1:250
B103	Upper homes +6.00	1:250
B104	Roof limits +9.00	1:250
B105	Undercroft -3.00	1:250
B200	Typical block: ground and gallery	1:125
B201	Typical block: upper and roof	1:125
B300	H1 through flat / clear room sizes	1:25
B301	H2 maisonette / both levels	1:50 / 1:25
B302	Public and private stair construction	1:25
B400	Home elevations / facade bay	1:50 / 1:25
B401	Building and stair sections	1:100 / 1:25
B500	Shops / court / openings	1:100
B600	Landscape / wetness / light positions	1:250
B700	Blender assembly / material details	1:25 / NTS

WHAT IS FIXED

144 × 120 m site. Four 36 × 18 m blocks. Eight public stair cores. Eight H1 flats and eight H2 maisonettes. Existing block origins and site routes are retained.

WHAT B01 RESOLVES

Wall faces, clear halls, door and window apertures, stair nosings, upper slab holes, mirrored southern modules and object coordinates. These details supersede schematic Rev 01 massing.

WHAT CLAUDE MUST PROVE

Actual capsule movement, headroom, full route widths, bot floor selection, spawn visibility and measured GPU performance. The drawings are a game modelling specification, not evidence of a playable 32-person map.

MODEL SOURCE ORDER

map.json owns site placement; build-spec.json owns detailed modules. Use the separate blueprint guide .blend for setting-out. Preserve the earlier massing and current Heron Court game.

DIMENSION CONVENTION

Metres. Home dimensions are CLEAR inside faces; footprints are outside faces. Datum is finished floor level (FFL). Slabs lie below FFL. Dimensions govern over scaling an image.

COORDINATES

Map: x east, z south, y up. Blender: (x - 72, 60 - z, y). GLB: (x - 72, y, z - 60). Apply mirrors to all vertices and openings, then recalculate normals.

DIMENSIONED GAME-ENVIRONMENT DESIGN

For Blender blockout / proposed / not an as-built playable

Dimensions govern. All lengths in metres unless marked mm. Print A1 at 100%.

ISSUE INDEX

SCALE 1:500 + NTS | PAPER 841 × 594 mm

MAP REV 01 + DETAIL ISSUE B01 / 18 OCTOBER 2026

DRAWN FROM METRIC DATA

build-spec.json + map.json


No networking / no runtime change

B000

B01 / ONSITE

ONSITE / HERON REACH

Datum +0.00 = ground finished floor / origin NW corner / dimensions in metres

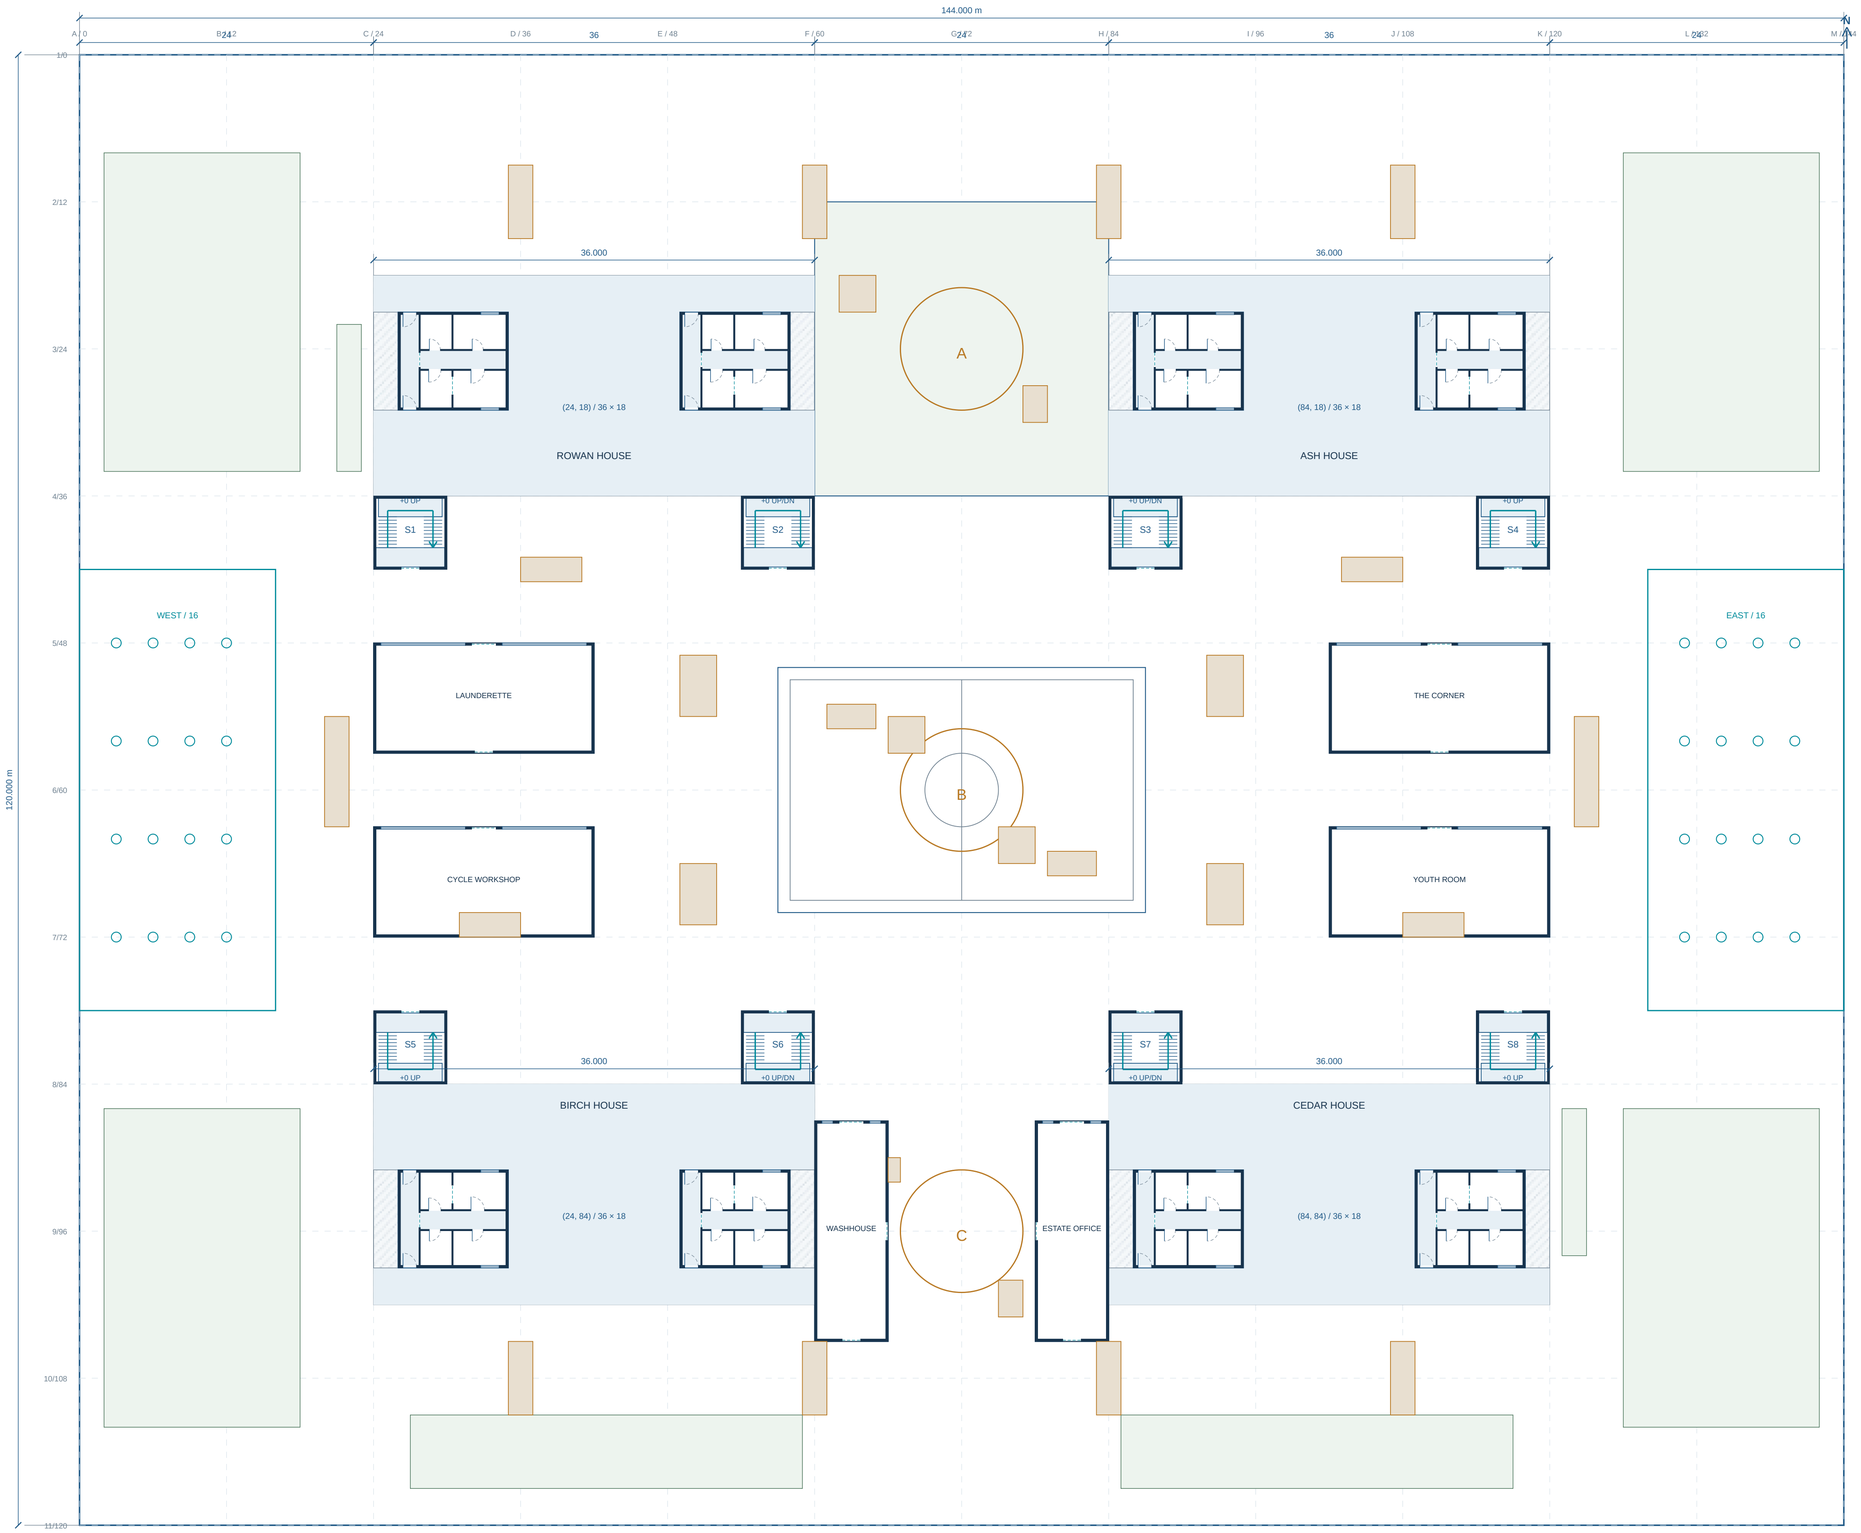

BLOCK	X	Z	W × D
NW	24	18	36 × 18
NE	84	18	36 × 18
SW	24	84	36 × 18
SE	84	84	36 × 18

CORE	X	Z	LEVELS
S1	24	36	0/3/6/9
S2	54	36	-3/0/3/6/9
S3	84	36	-3/0/3/6
S4	114	36	0/3/6
S5	24	78	0/3/6
S6	54	78	-3/0/3/6
S7	84	78	-3/0/3/6/9
S8	114	78	0/3/6/9

SETTING-OUT RULE

All rect arrays are [minimum x, minimum z, width, depth]. Core envelopes are 6 × 6. Home envelopes are 9 × 8. Origin pins are not mesh centres.

REPEATABLE GRID

Site grid A–M / 1–11 at 12 m. Facade subgrid 3 m. Core and doorway coordinates take precedence over a snapped decorative grid.

LEVEL DATUMS

B1 -3.00 / G 0.00 / L1 +3.00 / L2 +6.00 / R +9.00. Core roofs are +2.80 above their highest served FFL; they are not playable decks.

1:250 AT A1 / METRES

0 — 10 — 20 m

DIMENSIONED GAME-ENVIRONMENT DESIGN

For Blender blockout / proposed / not an as-built playable

Dimensions govern. All lengths in metres unless marked mm. Print A1 at 100%.

SITE SETTING OUT

SCALE 1:250 | PAPER 841 × 594 mm

MAP REV 01 + DETAIL ISSUE B01 / 18 OCTOBER 2026

DRAWN FROM METRIC DATA

build-spec.json + map.json

No networking / no runtime change


B100

B01 / ONSITE

ONSITE / HERON REACH

Finished floor +0.00 m / plans show proposed geometry / details B200–B500

B101 / GROUND FLOOR

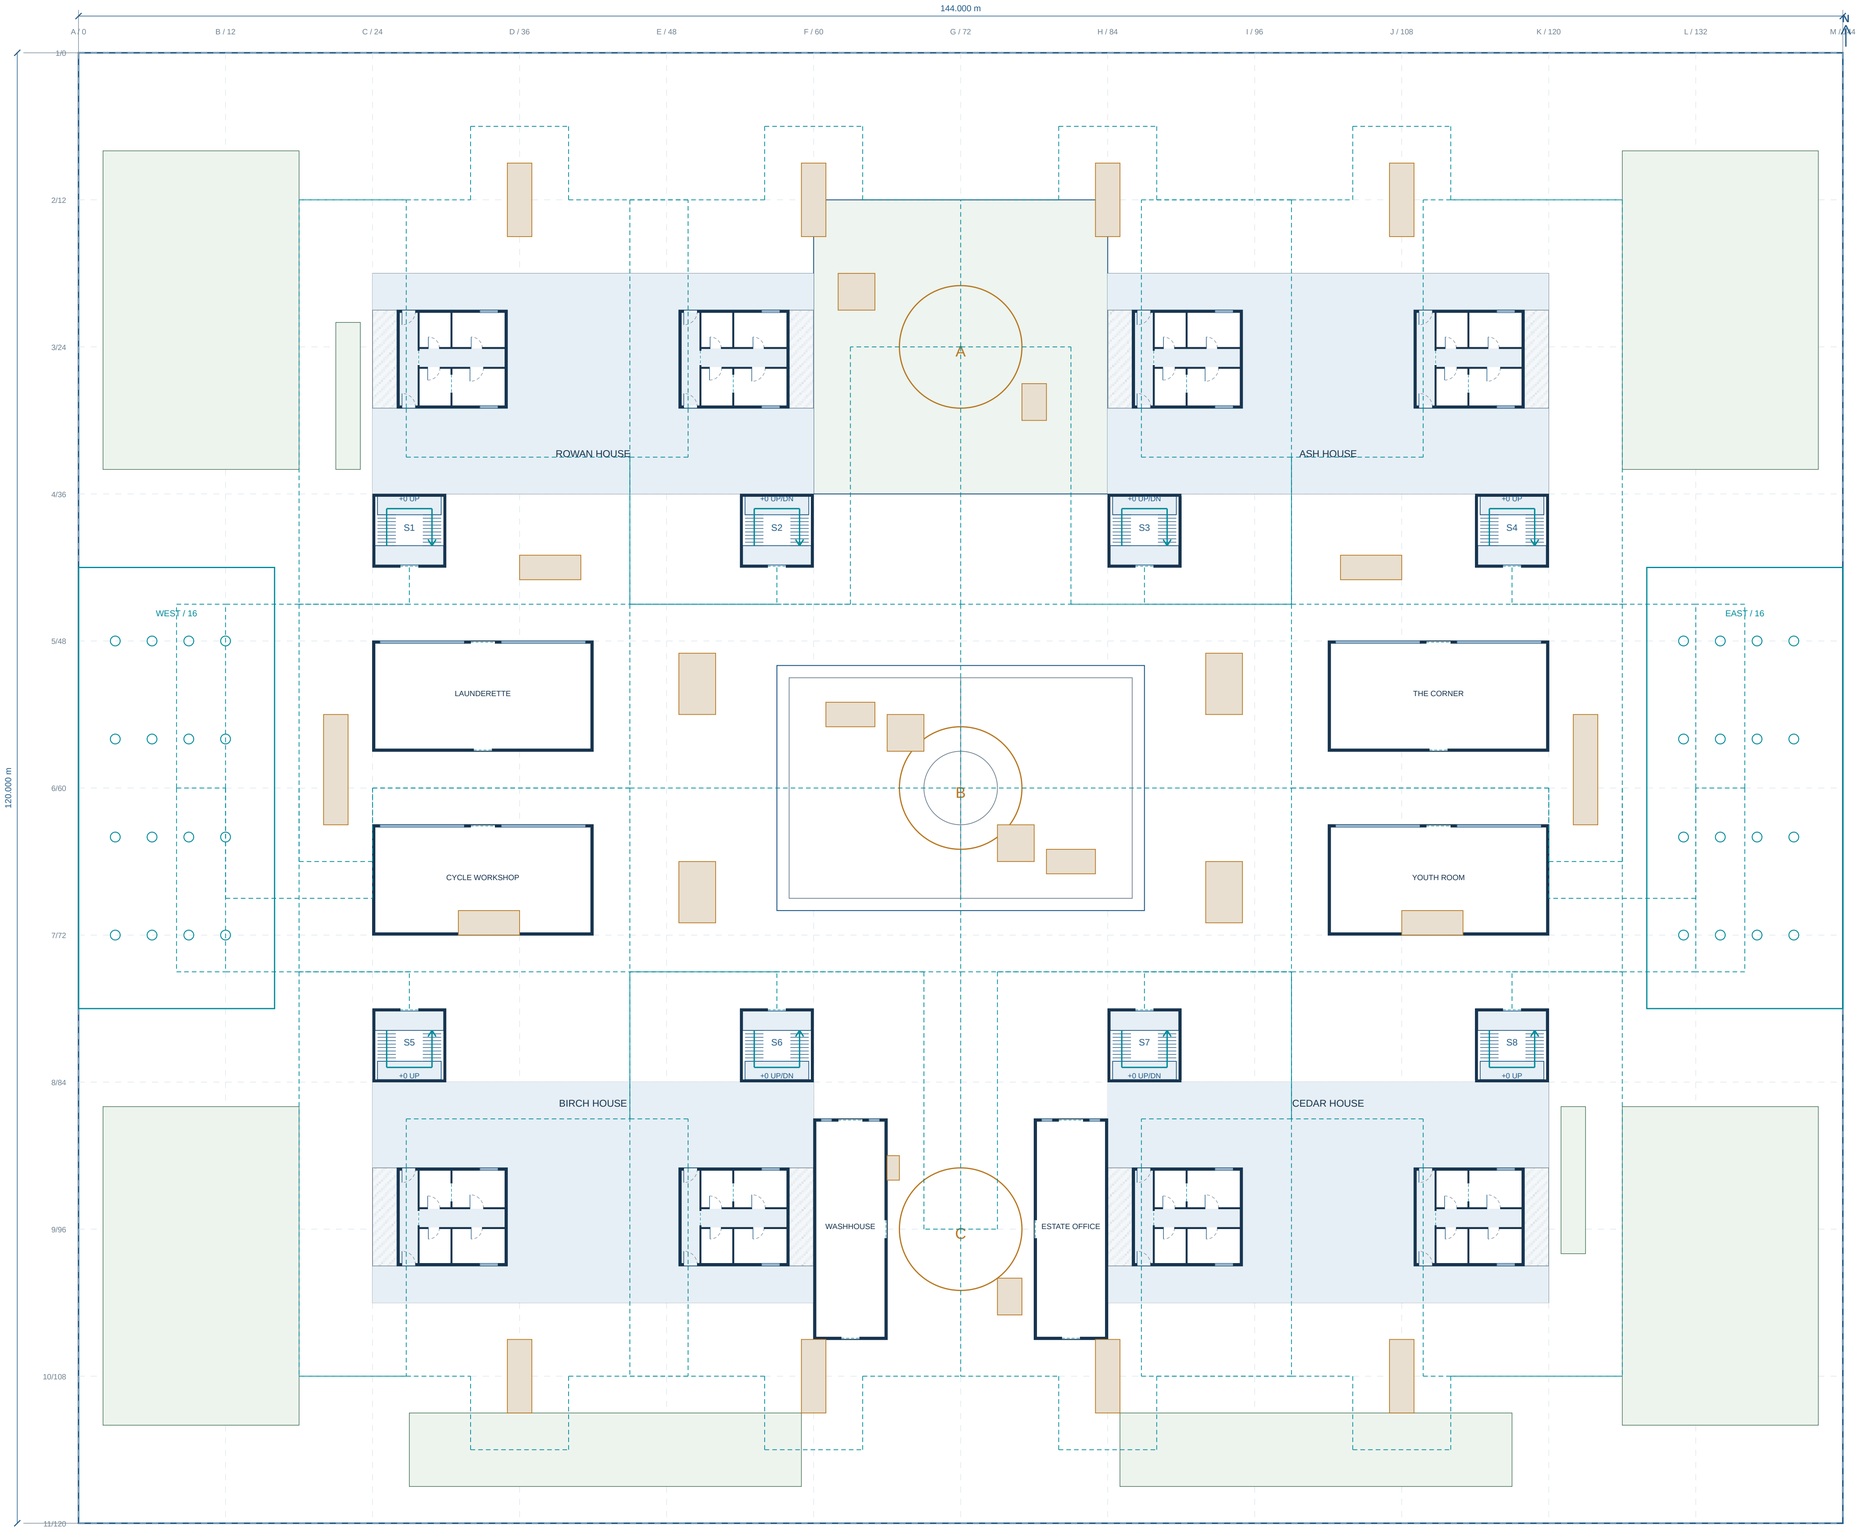

PLAYABLE GROUND

Continuous estate ground around the blocks. A Garden Court, B The Cage and C Washhouse Square are ground-only contest areas. Staging positions are initial placements, not dynamic respawns.

HOME AND SHOP OPENINGS

Eight H1 flats each have two through-hall exits. Six community/shop shells have explicit portals; B500 gives apertures. Windows are closed glazing, not player routes.

PUBLIC FLOOR

Pale blue means circulation. Hatched reserved strips are solid/service frontage. Ground cross-arcades remain open. Read H1 partitions at B300, not from this small-scale plan.

DRAWING KEY

Heavy navy: cut wall. Pale blue: circulation/slab. Dashed cyan: previous route intent only. Amber: cover/objective. Hatch: reserved/closed/void as labelled. Routes still need physical verification.

1:250 AT A1 / METRES

0 — 10 — 20 m

DIMENSIONED GAME-ENVIRONMENT DESIGN

For Blender blockout / proposed / not an as-built playable

Dimensions govern. All lengths in metres unless marked mm. Print A1 at 100%.

GROUND FLOOR

SCALE 1:250 | PAPER 841 × 594 mm

MAP REV 01 + DETAIL ISSUE B01 / 18 OCTOBER 2026

DRAWN FROM METRIC DATA

build-spec.json + map.json

No networking / no runtime change


B101

B01 / ONSITE

ONSITE / HERON REACH

Finished floor +3.00 m / plans show proposed geometry / details B200–B500

B102 / GALLERY FLOOR

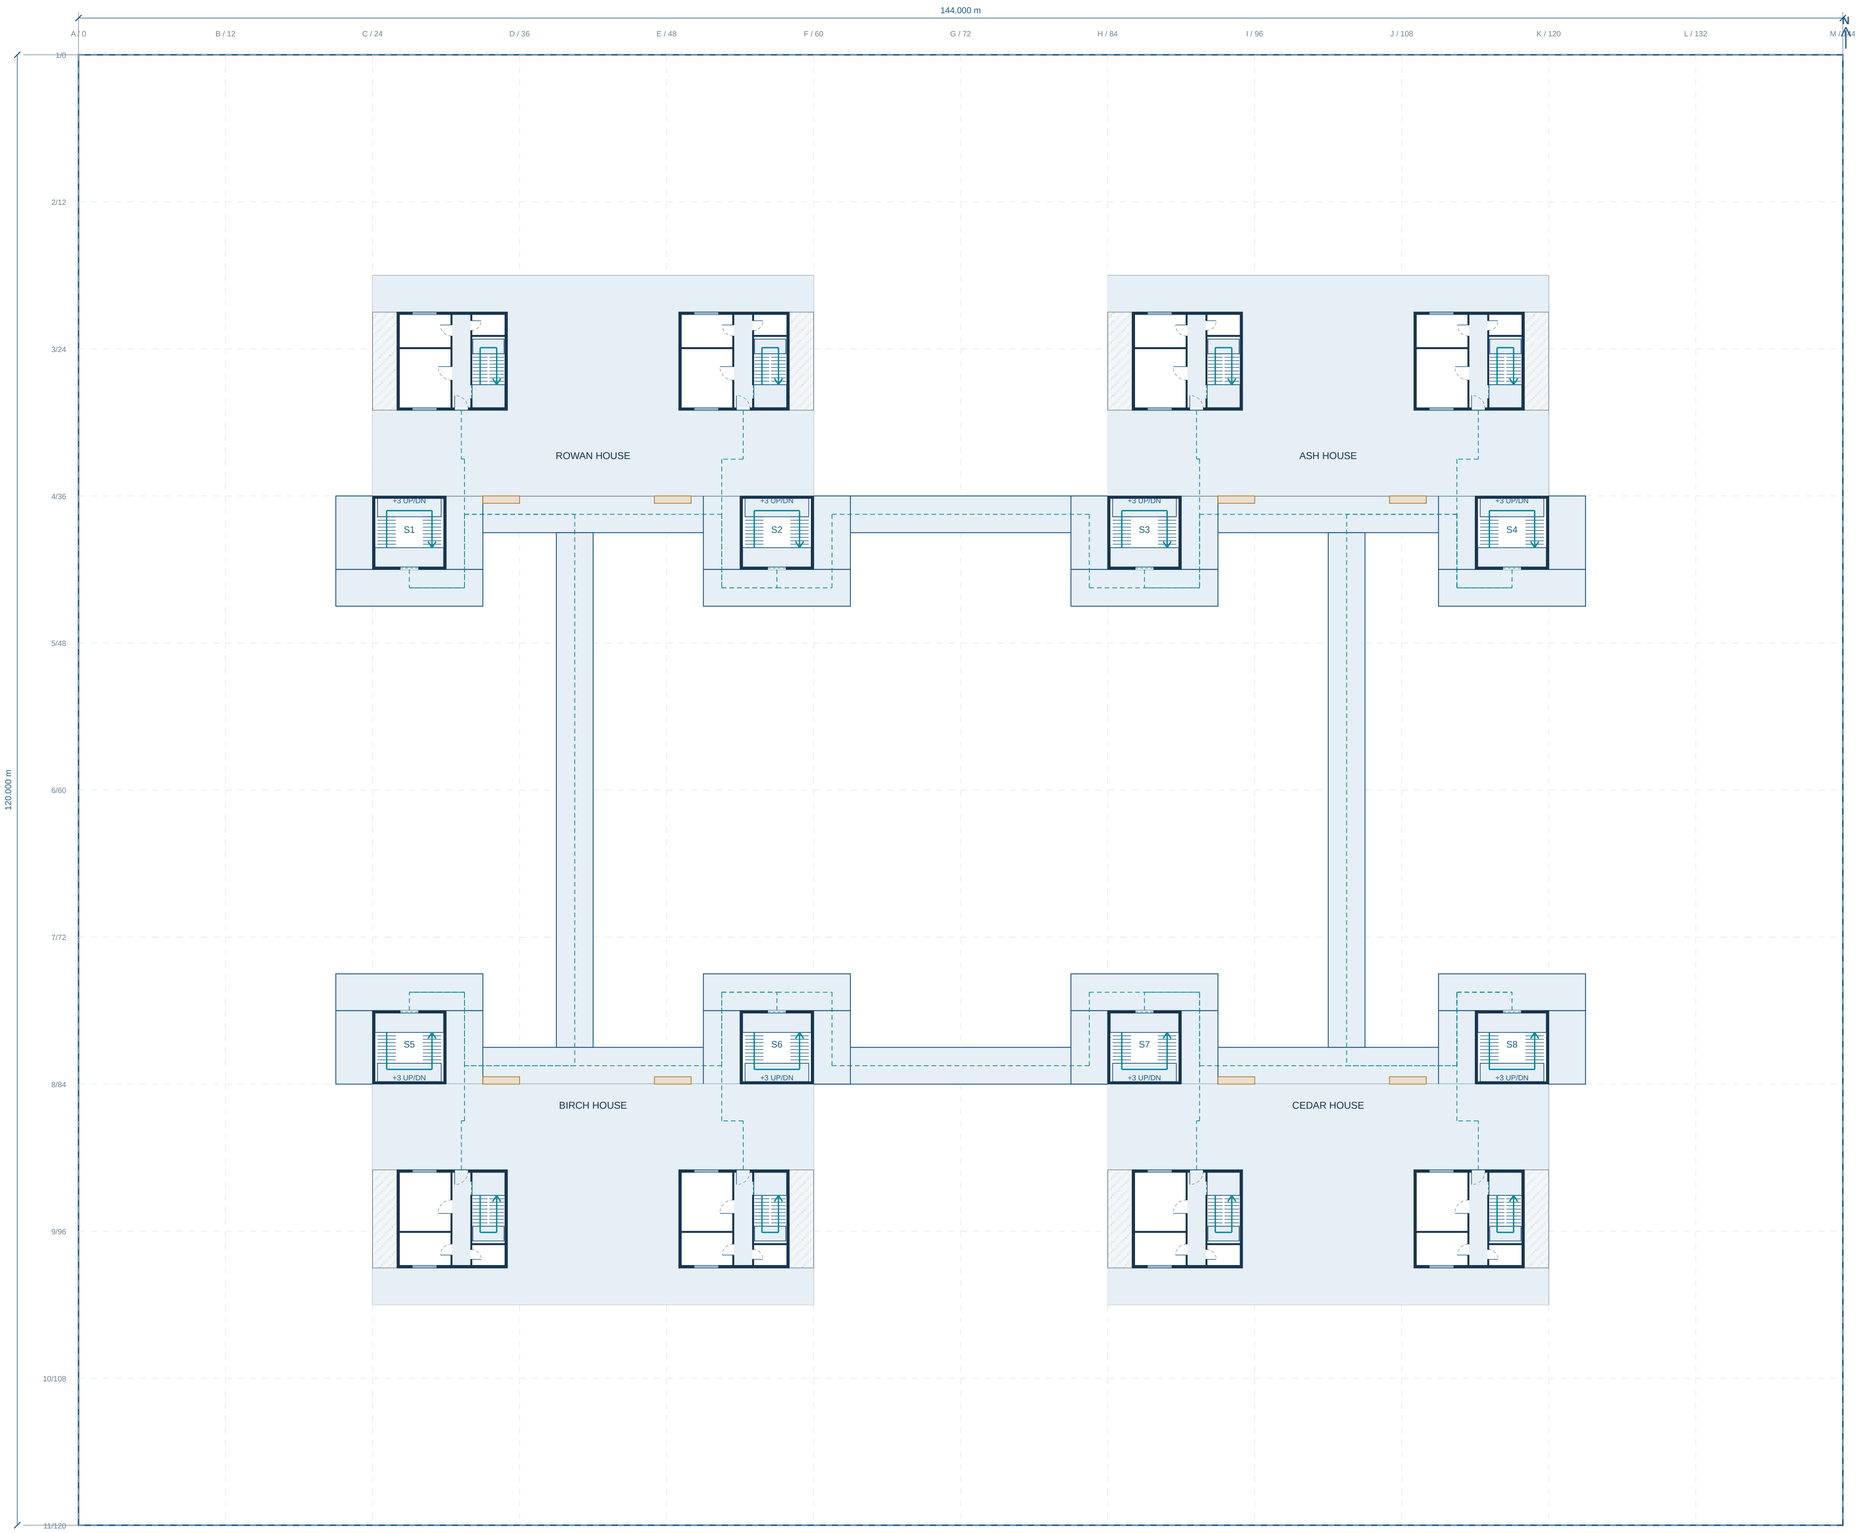

CONNECTED GALLERY

Continuous north/south links and east/west runs at +3.00. Public stairs exit onto wrapping aprons. Gallery width is 3.00 clear between guard faces.

MAISONETTE ENTRANCES

Eight H2 lower entrances face their block concourse. Upper exits are on +6.00 rear landings. Do not add a second door through a closed lower rear wall.

SLAB OPENINGS

Remove every served core footprint before adding its landing and stairs. Never bridge a flight with a gallery slab. See B302 for exact stair voids; use the union of overlapping floor areas.

DRAWING KEY

Heavy navy: cut wall. Pale blue: circulation/slab. Dashed cyan: previous route intent only. Amber: cover/objective. Hatch: reserved/closed/void as labelled. Routes still need physical verification.

1:250 AT A1 / METRES

0 — 10 — 20 m

DIMENSIONED GAME-ENVIRONMENT DESIGN

For Blender blockout / proposed / not an as-built playable

Dimensions govern. All lengths in metres unless marked mm. Print A1 at 100%.

GALLERY FLOOR

SCALE 1:250 | PAPER 841 × 594 mm

MAP REV 01 + DETAIL ISSUE B01 / 18 OCTOBER 2026

DRAWN FROM METRIC DATA

build-spec.json + map.json

No networking / no runtime change


B102

B01 / ONSITE

ONSITE / HERON REACH

Finished floor +6.00 m / plans show proposed geometry / details B200–B500

B103 / UPPER HOMES

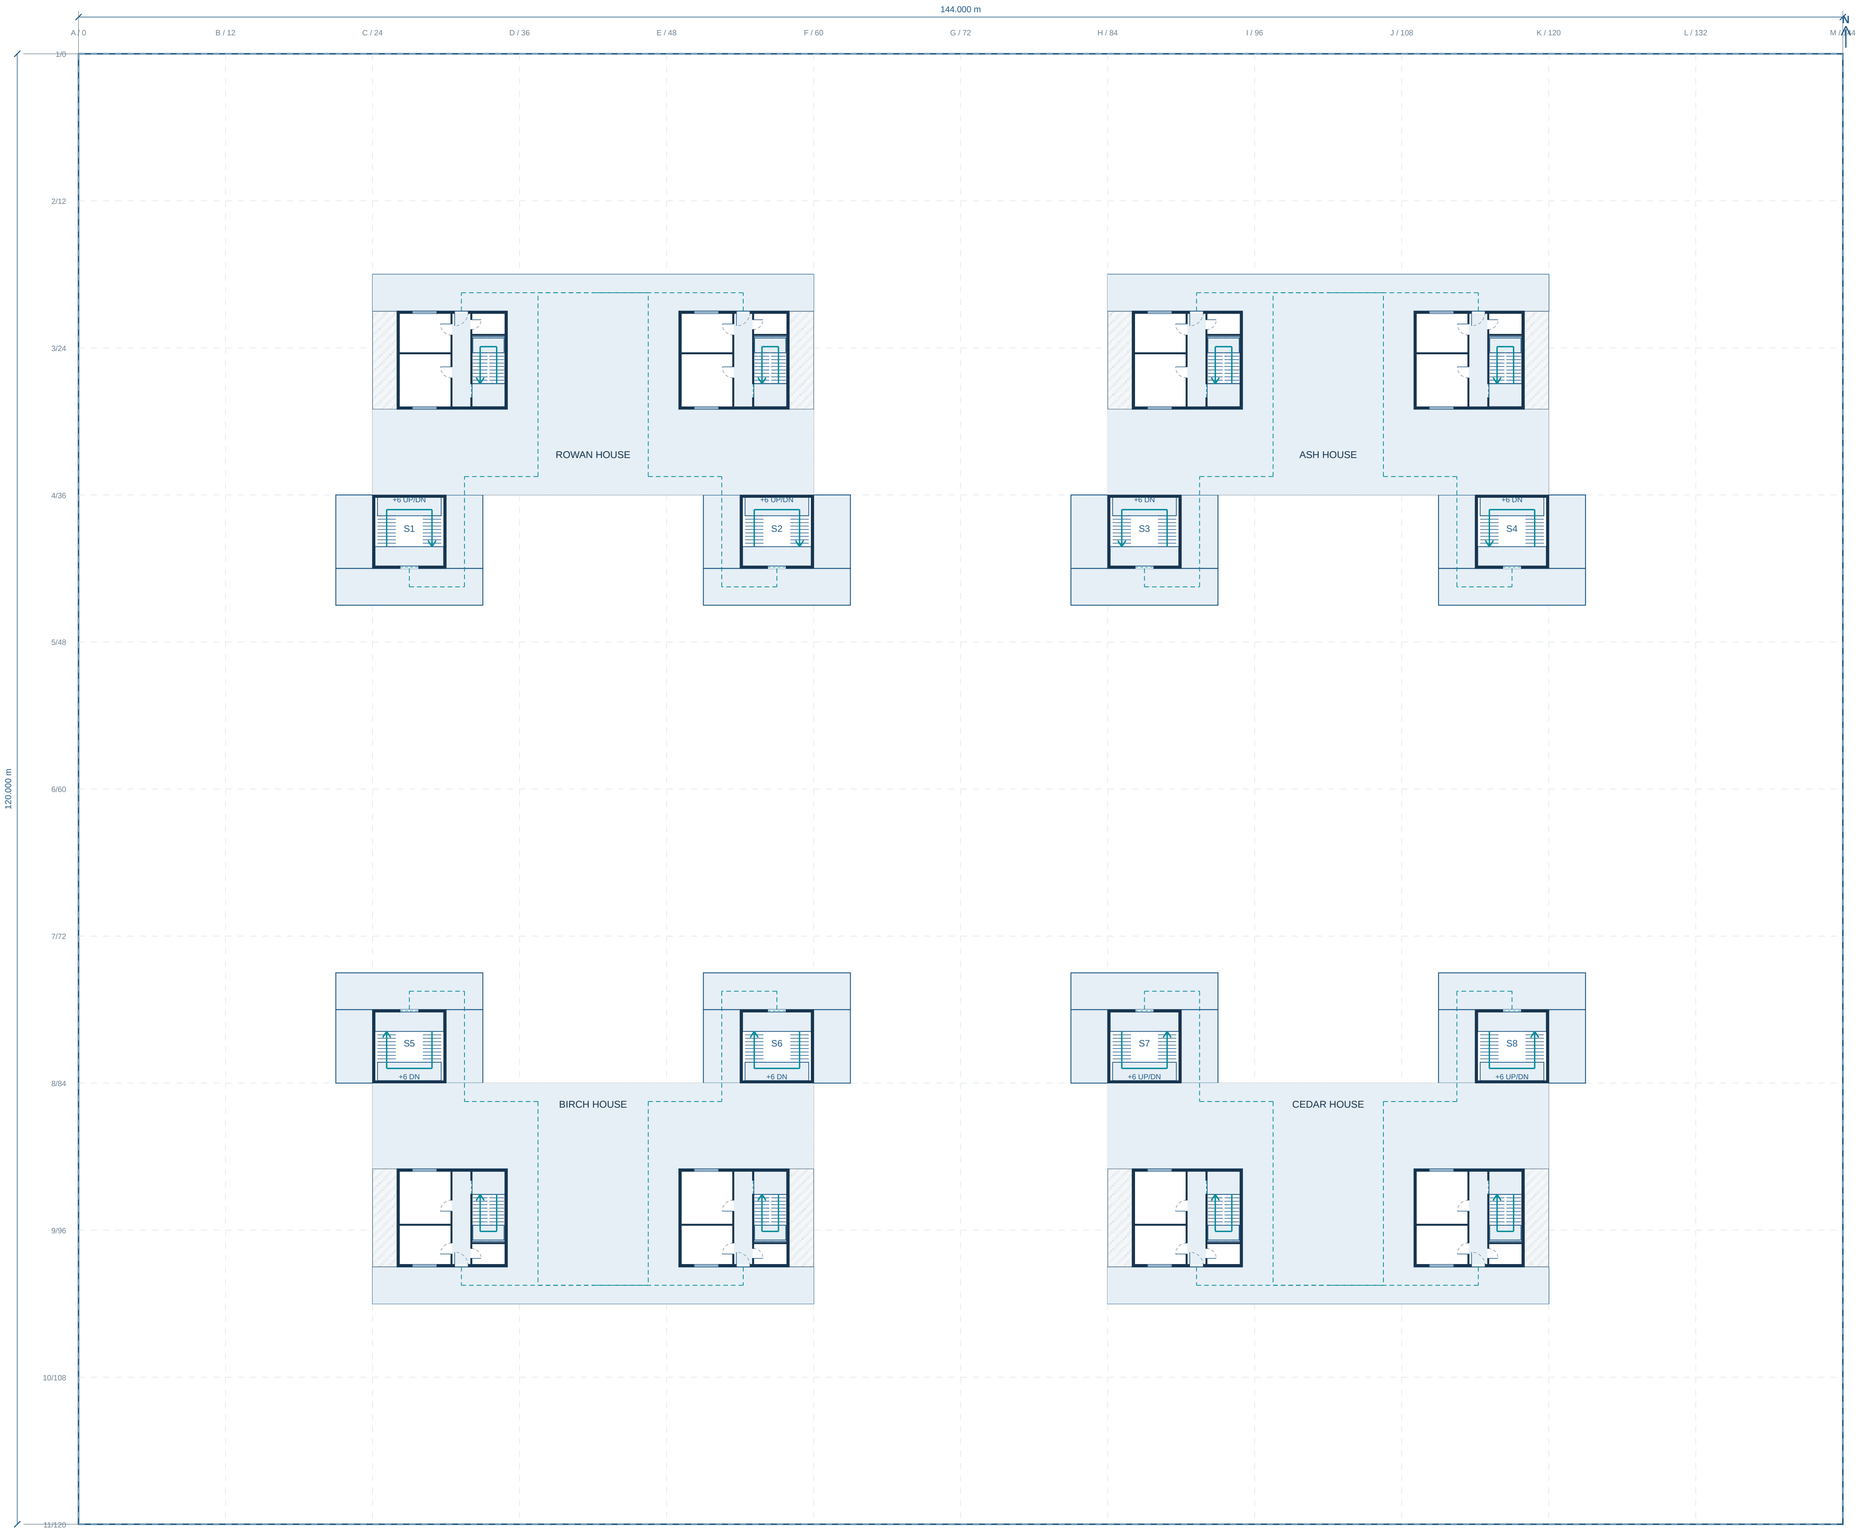

FOUR UPPER ISLANDS

No cross-court deck exists at +6.00. Each block connects two public cores and two H2 upper exits via shared/rear halls. The gaps between blocks remain open sky.

PRIVATE STAIR VOIDS

H2 upper slabs have 2.68 × 3.84 openings in their local coordinates. The top landing remains solid. Mirror openings with the entire southern home; see B301.

RESERVED FRONTAGE

Hatched strips are non-traversable service frontage. Every required route stays in the drawn common halls, homes or external landing aprons.

DRAWING KEY

Heavy navy: cut wall. Pale blue: circulation/slab. Dashed cyan: previous route intent only. Amber: cover/objective. Hatch: reserved/closed/void as labelled. Routes still need physical verification.

1:250 AT A1 / METRES

0 — 10 — 20 m

DIMENSIONED GAME-ENVIRONMENT DESIGN

For Blender blockout / proposed / not an as-built playable

Dimensions govern. All lengths in metres unless marked mm. Print A1 at 100%.

UPPER HOMES

SCALE 1:250 | PAPER 841 × 594 mm

MAP REV 01 + DETAIL ISSUE B01 / 18 OCTOBER 2026

DRAWN FROM METRIC DATA

build-spec.json + map.json

No networking / no runtime change


B103

B01 / ONSITE

ONSITE / HERON REACH

Finished floor +9.00 m / plans show proposed geometry / details B200–B500

B104 / ROOF PLAN

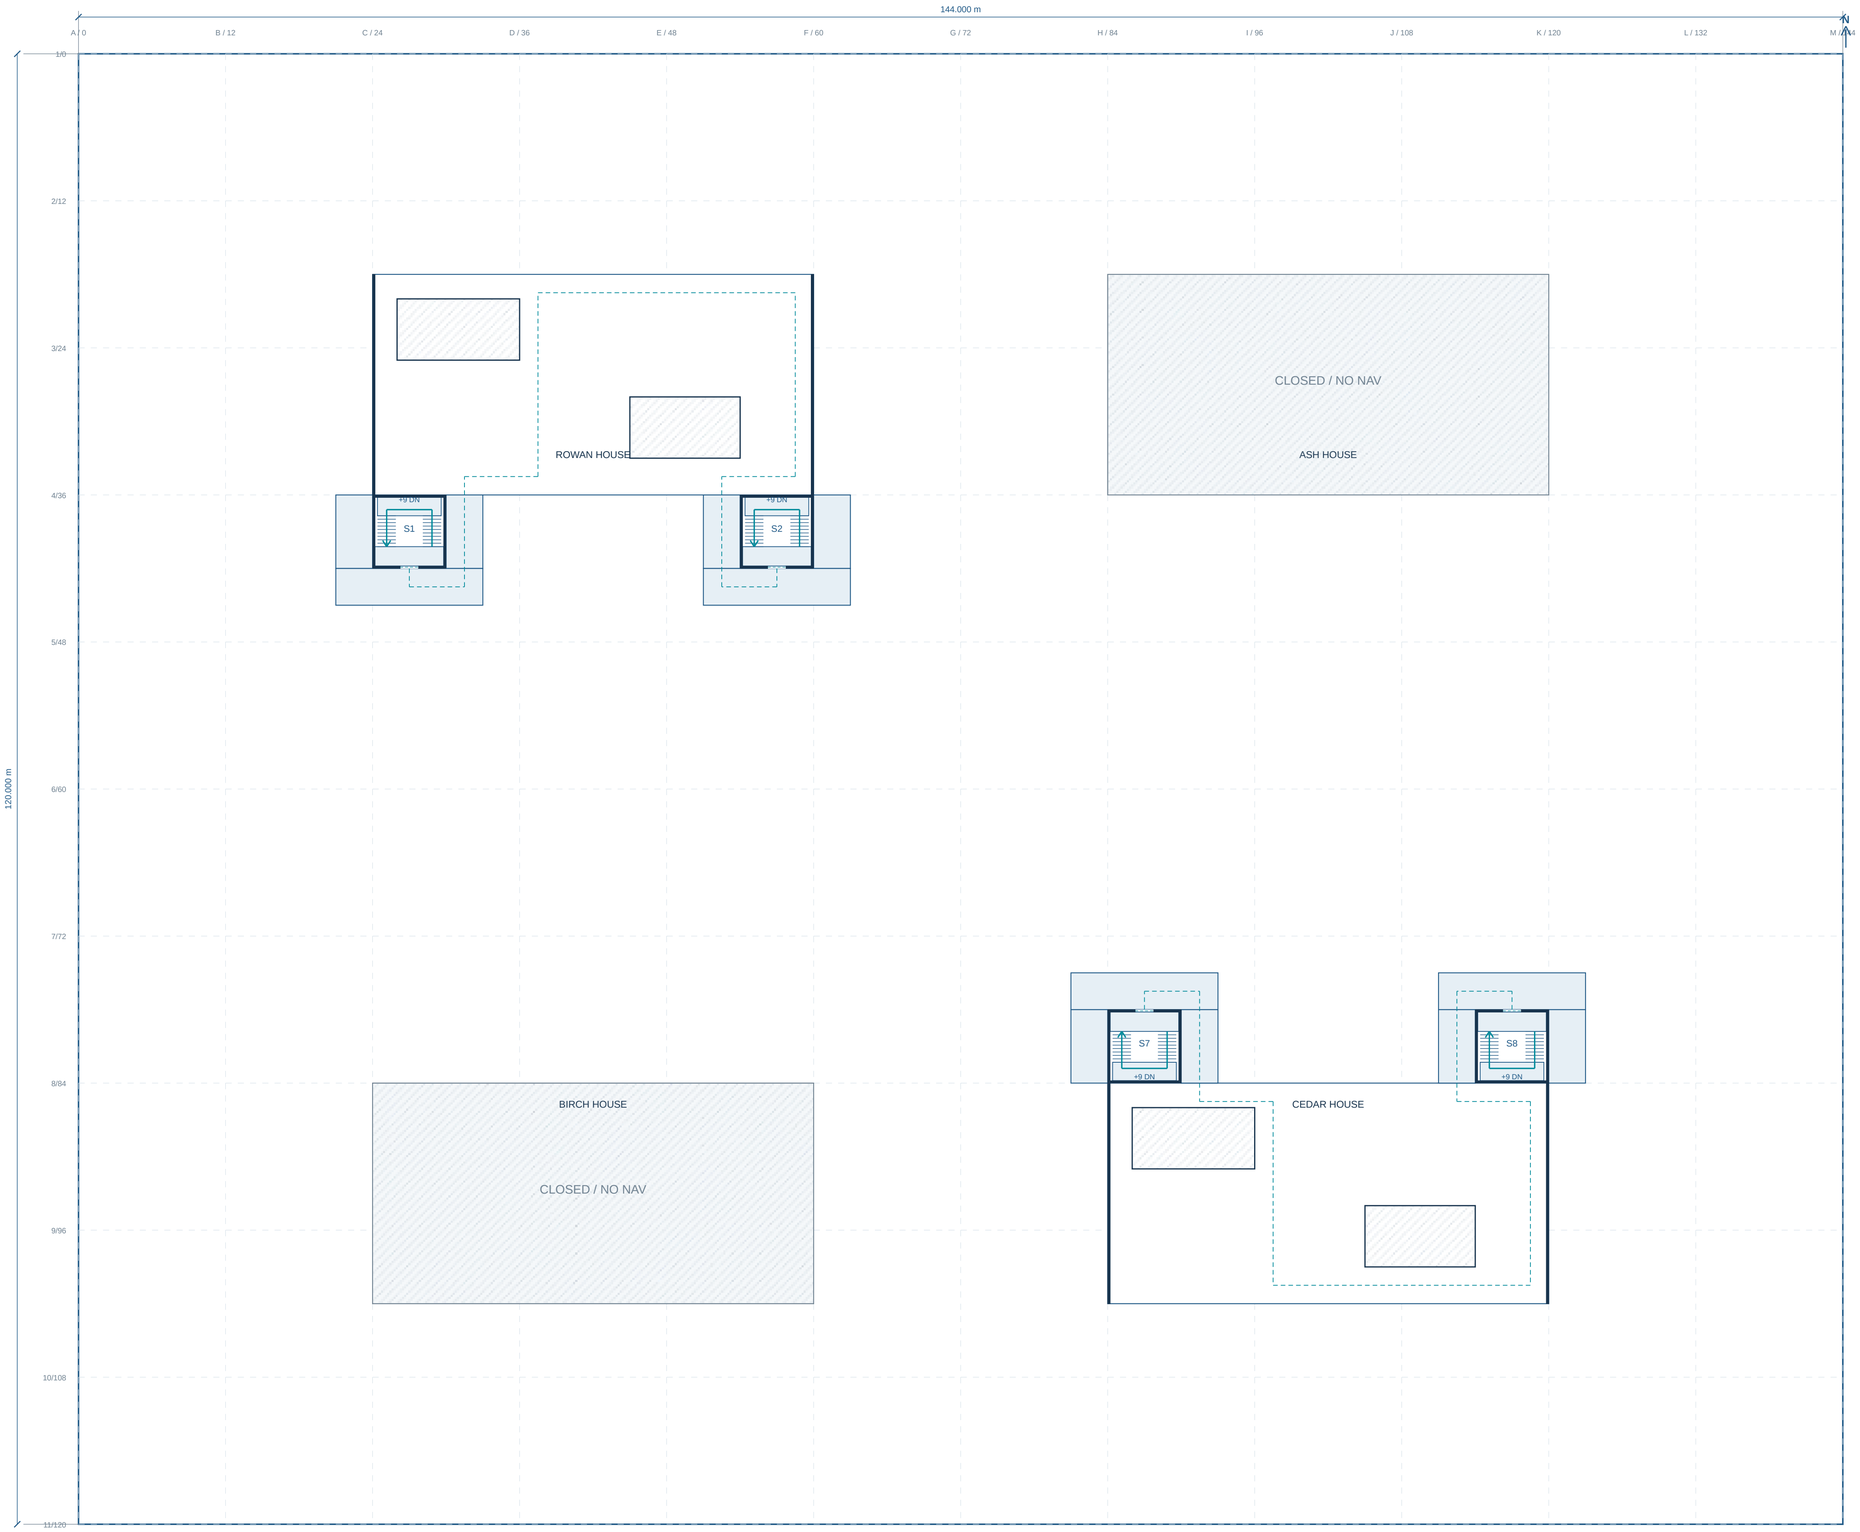

LIMITED ROOF ACCESS

Rowan NW and Cedar SE terraces only. Two public core exits per terrace. Ash NE and Birch SW roofs remain closed; do not add nav surfaces or jump routes there.

GUARDS AND SCREENS

Guard all exposed edges to 1.20. Keep the existing 2.10 opaque outer side screens facing staging areas. Plant housings interrupt long views; placement remains a design target.

CORE OVERRUN

S1/S2/S7/S8 extend to a +11.80 cap above their +9.00 landing. No flight continues above +9.00. Other cores cap at +8.80; no fake route from them to a closed roof.

DRAWING KEY

Heavy navy: cut wall. Pale blue: circulation/slab. Dashed cyan: previous route intent only. Amber: cover/objective. Hatch: reserved/closed/void as labelled. Routes still need physical verification.

1:250 AT A1 / METRES

0 — 10 — 20 m

DIMENSIONED GAME-ENVIRONMENT DESIGN

For Blender blockout / proposed / not an as-built playable

Dimensions govern. All lengths in metres unless marked mm. Print A1 at 100%.

ROOF PLAN

SCALE 1:250 | PAPER 841 × 594 mm

MAP REV 01 + DETAIL ISSUE B01 / 18 OCTOBER 2026

DRAWN FROM METRIC DATA

build-spec.json + map.json

No networking / no runtime change


B104

B01 / ONSITE

ONSITE / HERON REACH

Finished floor -3.00 m / plans show proposed geometry / details B200–B500

B105 / UNDERCROFT

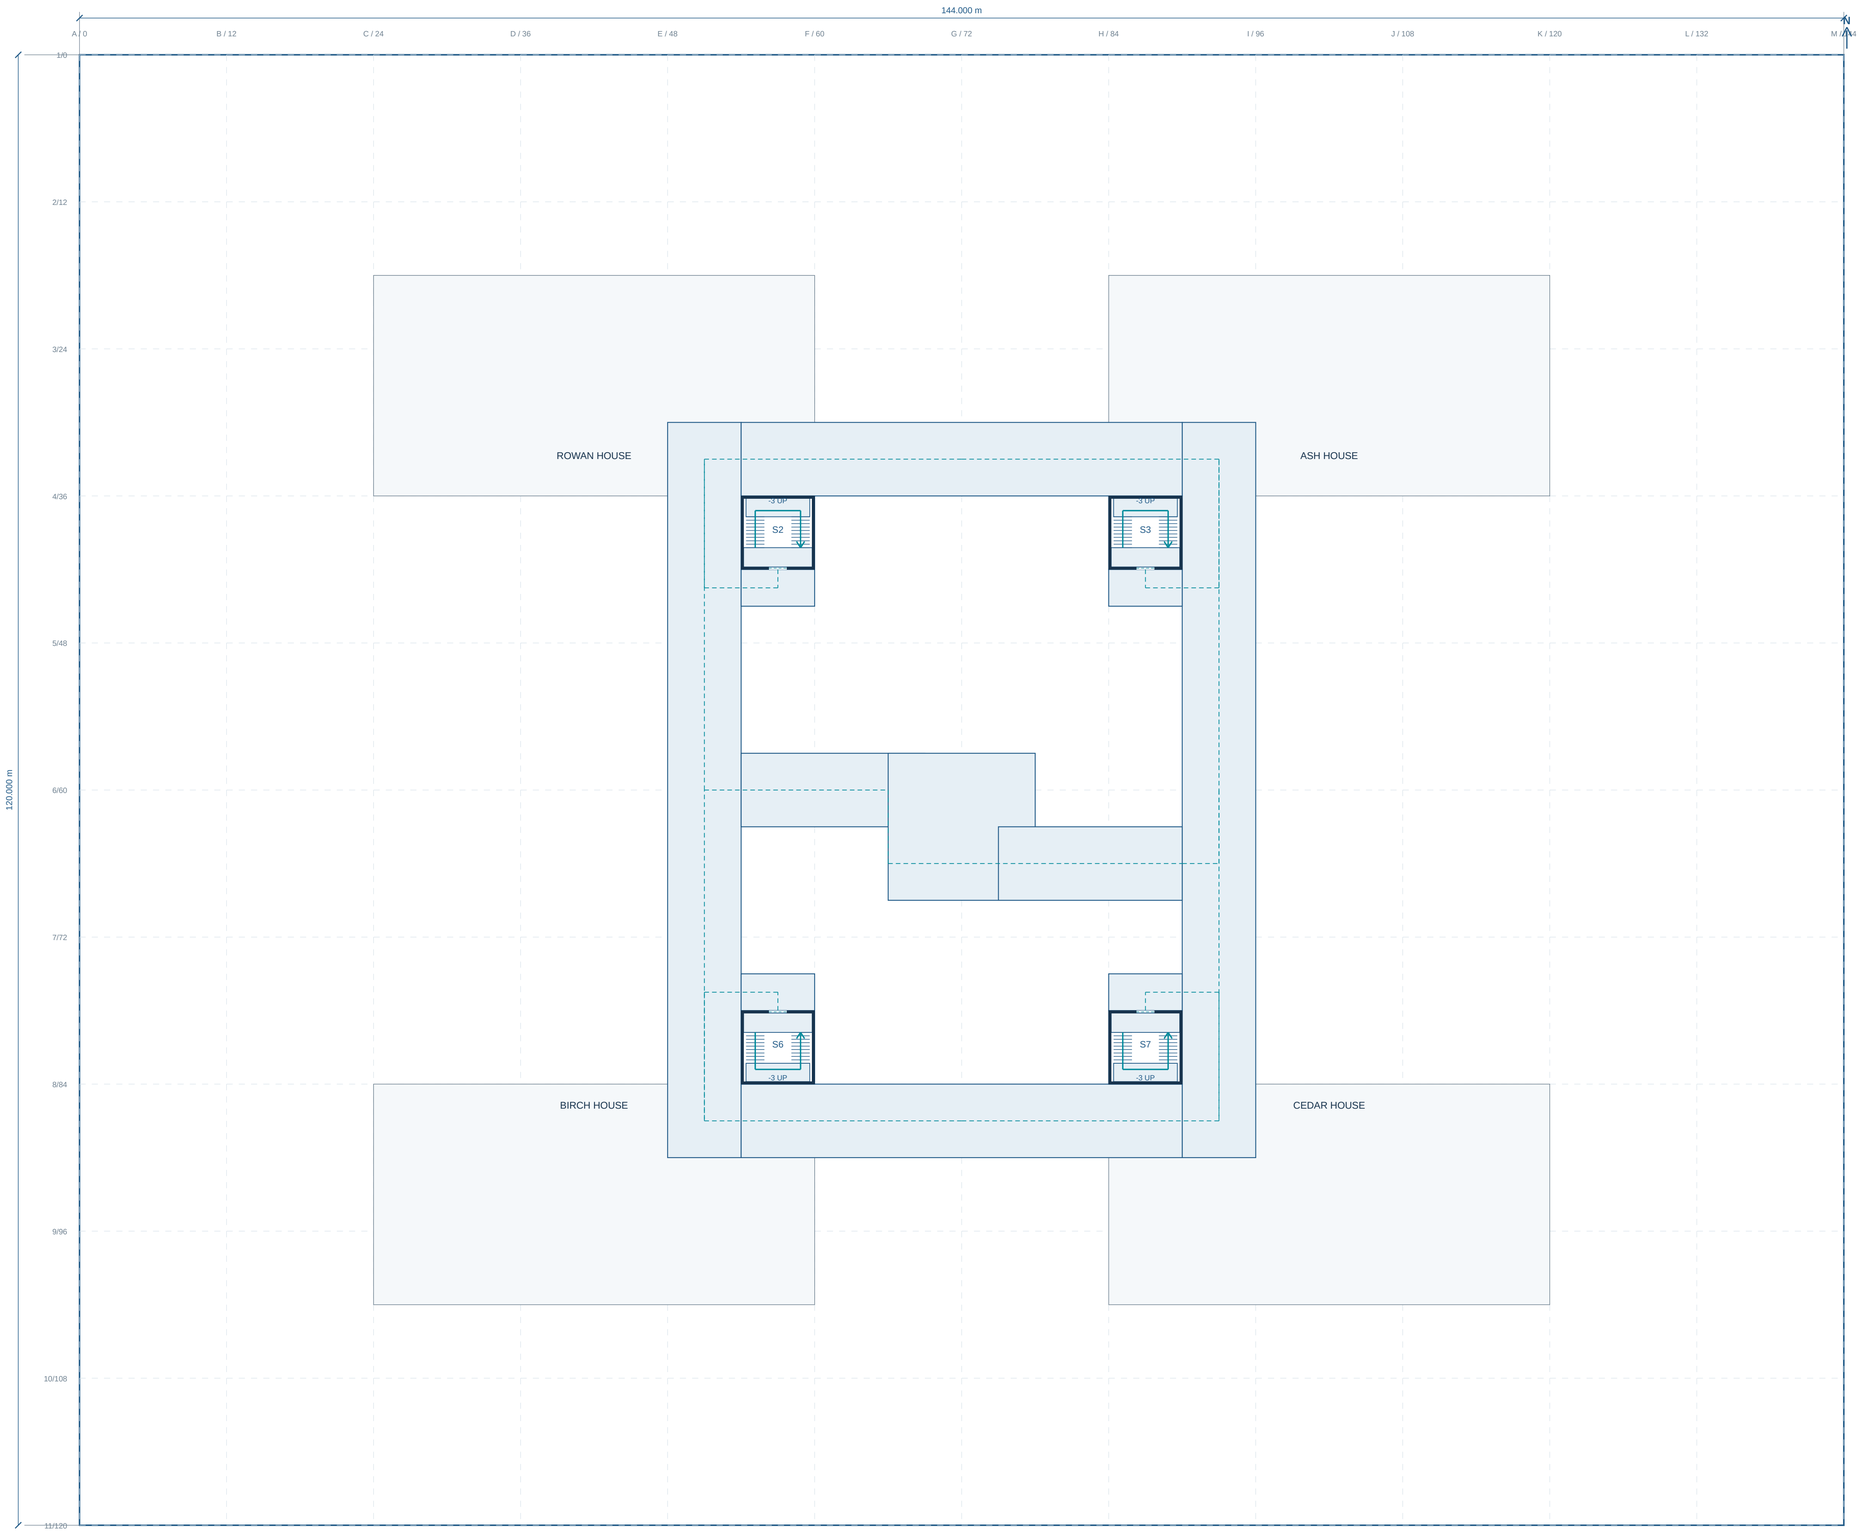

PARTIAL UNDERCROFT

Only blue areas are floor at -3.00. White/grey site context is not an underground slab. Four exits use S2, S3, S6 and S7; no underground spawn room.

WALLS AND CEILING

Build 200 mm walls outside the union boundary. Floor -3.00, ceiling underside -0.20. No internal wall at overlapping rectangle joins. Keep services above 2.40 clear.

STAIR CONNECTIONS

Core entry aprons connect the service loop to the full-level landing. Delete ground slabs over flights to G. Avoid sealing an entrance with an imported terrain plane.

DRAWING KEY

Heavy navy: cut wall. Pale blue: circulation/slab. Dashed cyan: previous route intent only. Amber: cover/objective. Hatch: reserved/closed/void as labelled. Routes still need physical verification.

1:250 AT A1 / METRES

0 — 10 — 20 m

DIMENSIONED GAME-ENVIRONMENT DESIGN

For Blender blockout / proposed / not an as-built playable

Dimensions govern. All lengths in metres unless marked mm. Print A1 at 100%.

UNDERCROFT

SCALE 1:250 | PAPER 841 × 594 mm

MAP REV 01 + DETAIL ISSUE B01 / 18 OCTOBER 2026

DRAWN FROM METRIC DATA

build-spec.json + map.json


No networking / no runtime change

B105

B01 / ONSITE

NW / G / FFL +0.00

36 × 18 block plus two cores and external landing aprons

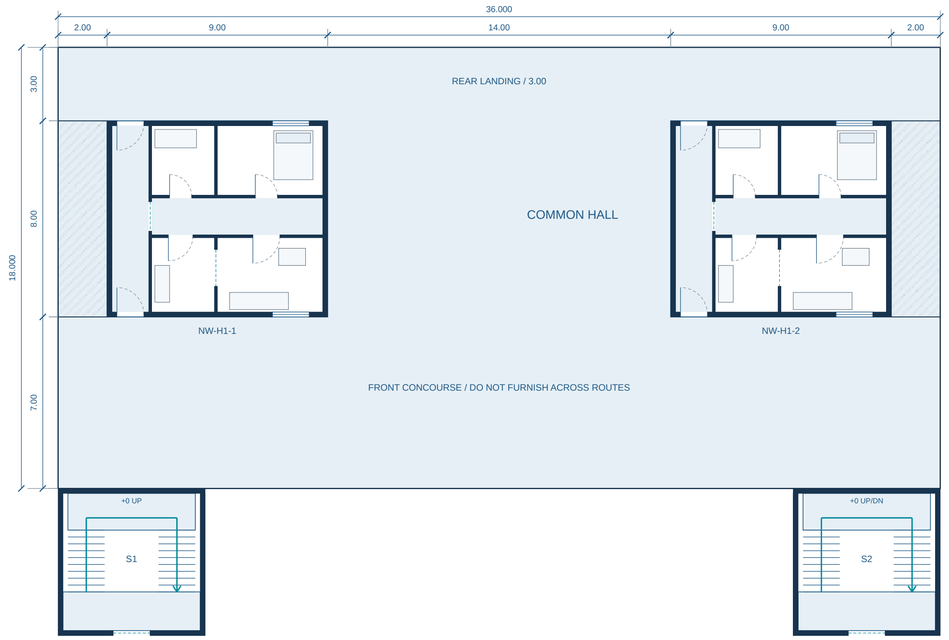


1:125 AT A1 / METRES

0 5 10 m

NW / L1 / FFL +3.00

36 × 18 block plus two cores and external landing aprons

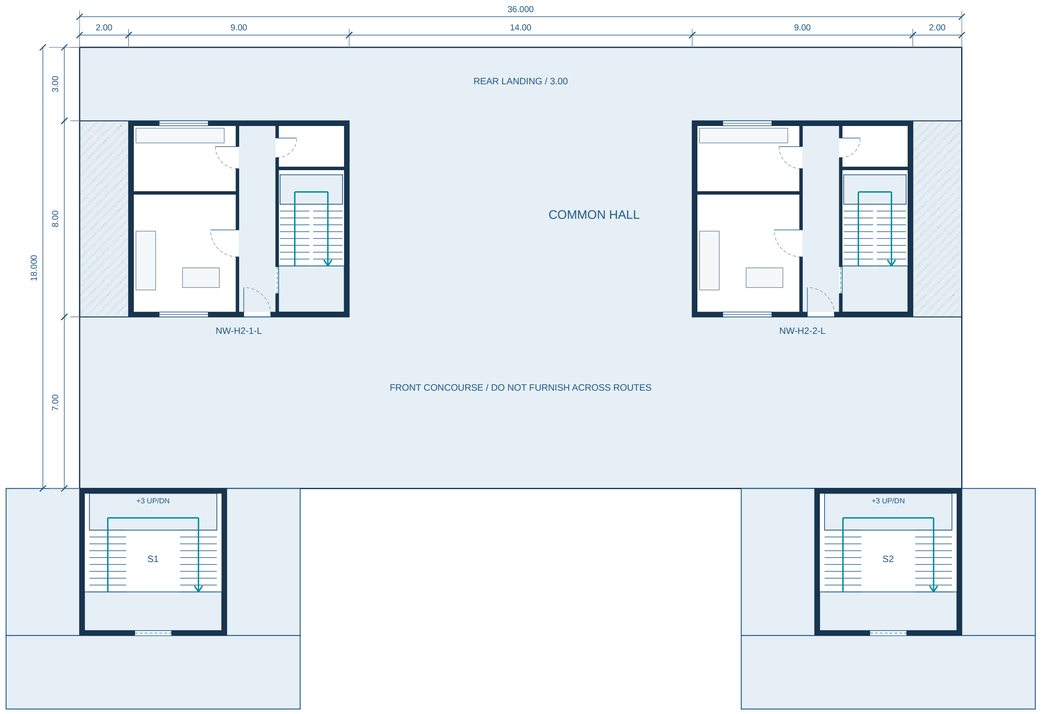

1:125 AT A1 / METRES

0 5 10 m

BLOCK ASSEMBLY

Set the block NW corner first. Homes sit at local (2,3) and (25,3), both 9 × 8. Front concourse starts local z=11; rear landing is z=0–3. Reserve only the two 2 × 8 side strips. Ground arcade at local x=18–24 stays clear.

SOUTHERN TRANSFORM

Birch/Cedar: world z = block z + 18 - local z. Home origins become local z=7, and home geometry mirrors within its 8 m footprint. Public stair origin is block z - 6; the stair entrance faces north. Do not rotate only the door labels.

FACADE TREATMENT


The broad blue areas are common concourses/landings, not extra flats. Open edges receive guards, brick piers and soffits; use glazing only where scheduled. Keep both sides of every home exit connected.

PORTALS AND BRIDGES

No wall crosses a shared hall, stair apron or the ground arcade. At +3 the bridges connect between blocks. At +6 there is no inter-block bridge. All floor plates are unions with holes, not overlapping coplanar rectangles.

NW / L2 / FFL +6.00

36 × 18 block plus two cores and external landing aprons

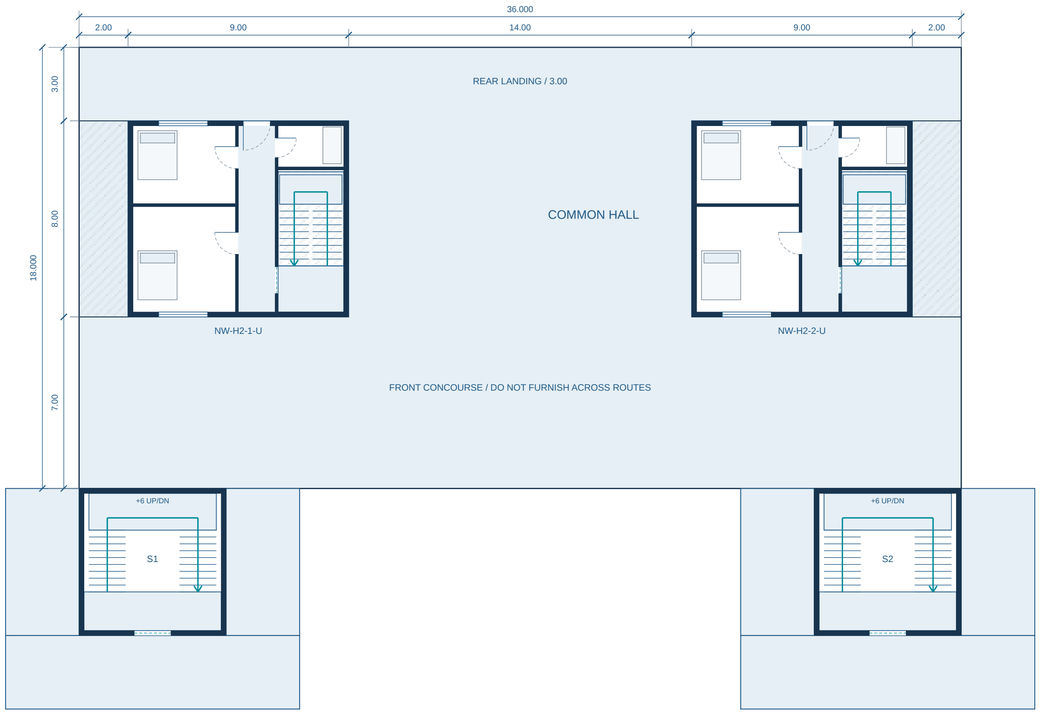


1:125 AT A1 / METRES

0 5 10 m

NW / R / FFL +9.00

36 × 18 block plus two cores and external landing aprons

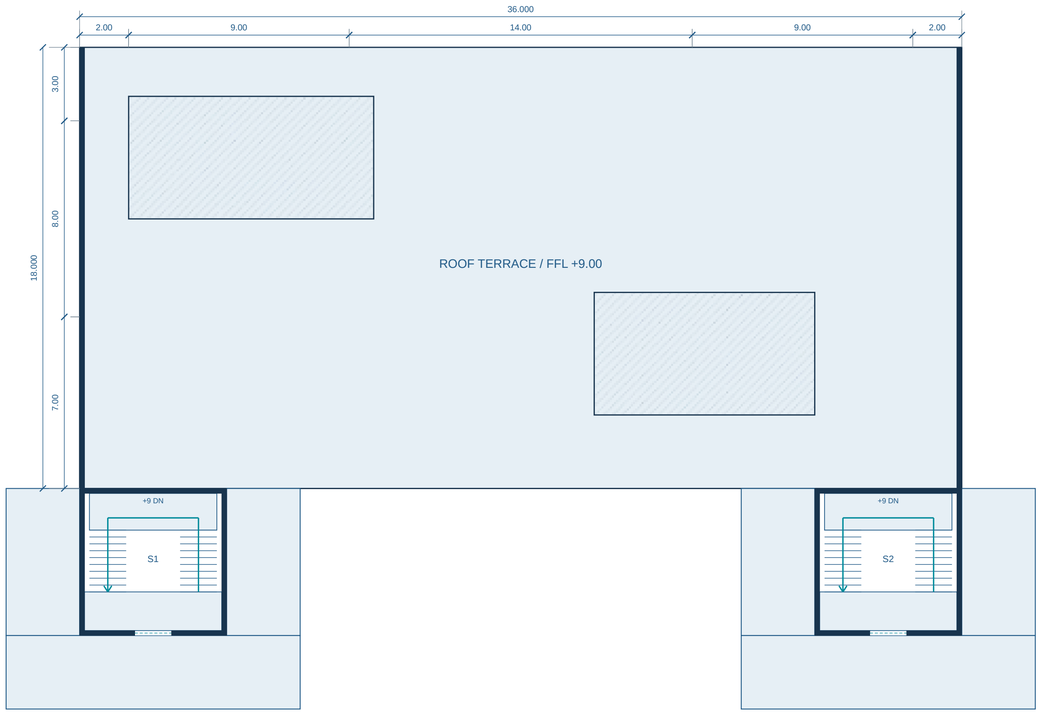

1:125 AT A1 / METRES

0 5 10 m

BLOCK ASSEMBLY

Set the block NW corner first. Homes sit at local (2,3) and (25,3), both 9 × 8. Front concourse starts local z=11; rear landing is z=0–3. Reserve only the two 2 × 8 side strips. Ground arcade at local x=18–24 stays clear.

SOUTHERN TRANSFORM

Birch/Cedar: world z = block z + 18 - local z. Home origins become local z=7, and home geometry mirrors within its 8 m footprint. Public stair origin is block z - 6; the stair entrance faces north. Do not rotate only the door labels.

FACADE TREATMENT

The broad blue areas are common concourses/landings, not extra flats. Open edges receive guards, brick piers and soffits; use glazing only where scheduled. Keep both sides of every home exit connected.


PORTALS AND BRIDGES

No wall crosses a shared hall, stair apron or the ground arcade. At +3 the bridges connect between blocks. At +6 there is no inter-block bridge. All floor plates are unions with holes, not overlapping coplanar rectangles.

ONSITE / HERON REACH

One-bedroom module / eight ground instances / 72 m² gross / clear dimensions between finished faces

B300 / H1 THROUGH FLAT

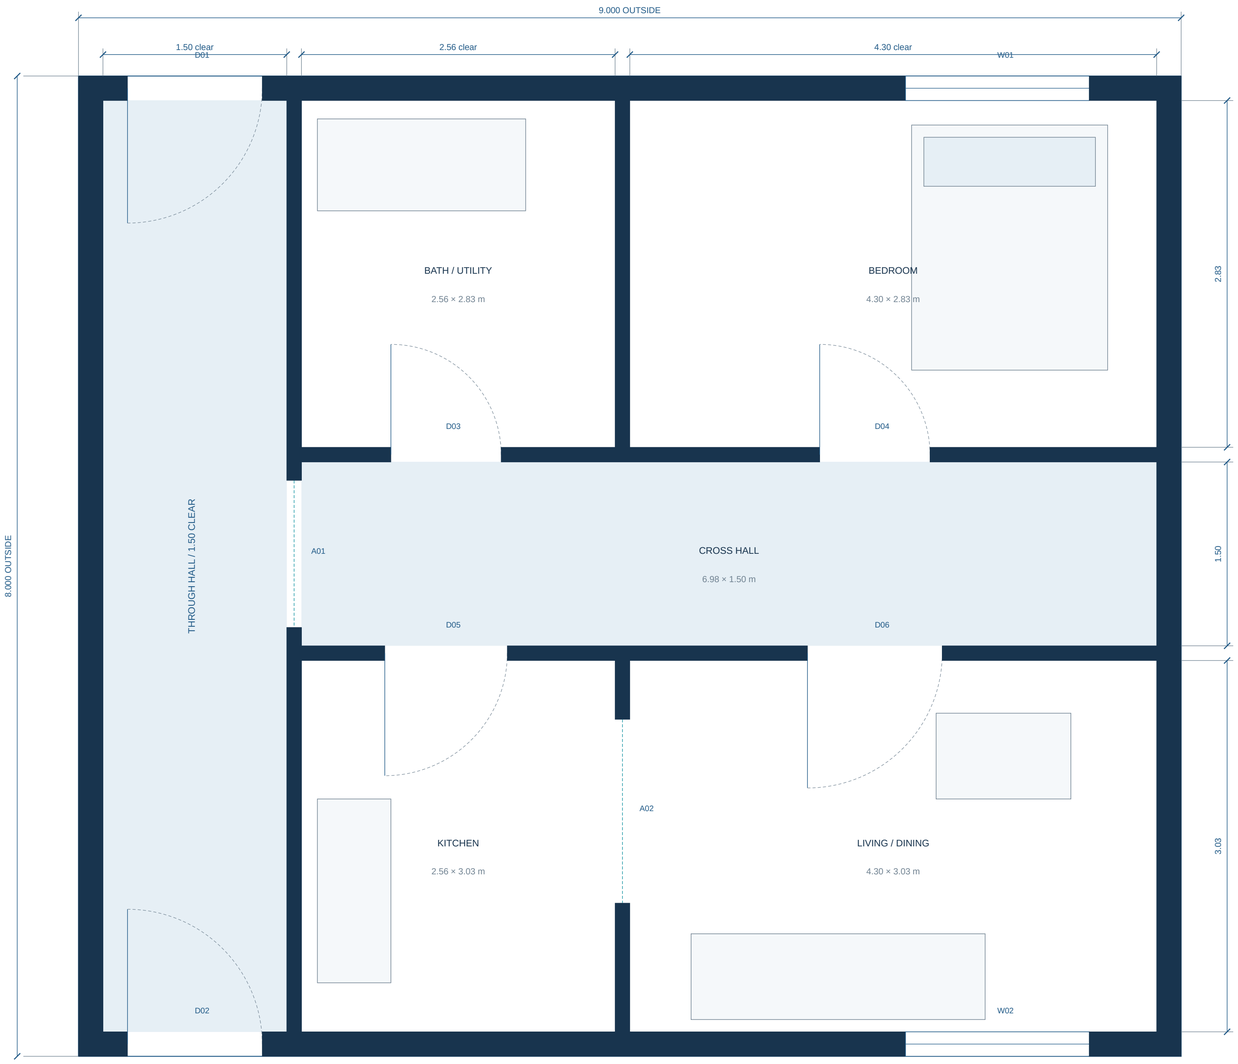

1:25 AT A1 / METRES

0 — 2.5 — 5 m

ROOM TAGS AND OPENINGS: use the local coordinates in build-spec.json. Each placed portal is listed in home-openings.csv with world position, width and head height. Door arcs are modelling guides; working-door gameplay is deferred.

ROOM	CLEAR W × D	AREA
THROUGH HALL	1.50 × 7.60	11.40 m²
BATH / UTILITY	2.56 × 2.83	7.25 m²
BEDROOM	4.30 × 2.83	12.17 m²
CROSS HALL	6.98 × 1.50	10.47 m²
KITCHEN	2.56 × 3.03	7.76 m²
LIVING / DINING	4.30 × 3.03	13.03 m²

OPENING	WIDTH	HEAD / SILL
D01 / door	1.10	2.20 / 0.00
W01 / window	1.50	2.25 / 0.90
D02 / door	1.10	2.20 / 0.00
W02 / window	1.50	2.25 / 0.90
A01 / arch	1.20	2.20 / 0.00
D03 / door	0.90	2.20 / 0.00
D04 / door	0.90	2.20 / 0.00
D05 / door	1.00	2.20 / 0.00
D06 / door	1.10	2.20 / 0.00
A02 / arch	1.50	2.20 / 0.00

WALLS AND LEVELS

External shell 200 mm. Partitions 120 mm. FFL 0.00; clear ceiling +2.80, next FFL +3.00. Shell fits inside the 9 × 8 footprint. Slab top equals FFL; do not add slab thickness above it.

TWO REAL EXITS

D01/D02 are 1.10 clear and share a 1.50 clear hall. Hall centre is x=0.95; openings x=0.40–1.50. Door leaves are held open in the first blockout. Bedrooms/bathrooms are optional, not the through route.

MODELLING NOTES

Room dimensions exclude walls. Furniture is an allowance, not another collider owner. Preserve cross-hall and door sweeps. Window sill 0.90, head 2.25; closed glazing. Southern instances mirror every local z coordinate.

ONSITE / HERON REACH

Eight two-storey homes / 144 m² gross per home / lower gallery entrance and upper rear exit

B301 / H2 MAISONETTE

H2-L / +3.00




FRONT ENTRY +3.00

1:50 AT A1 / METRES



H2-U / +6.00

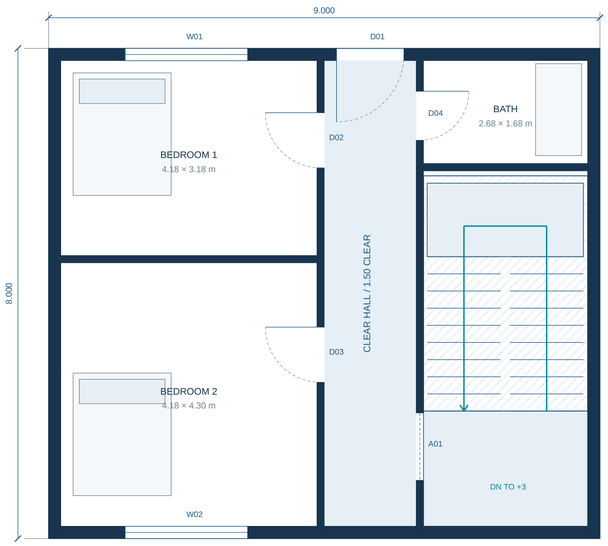


REAR EXIT +6.00 / VOID HATCHED

1:50 AT A1 / METRES



ST-H / 3 × 6 STAIR / 1:25

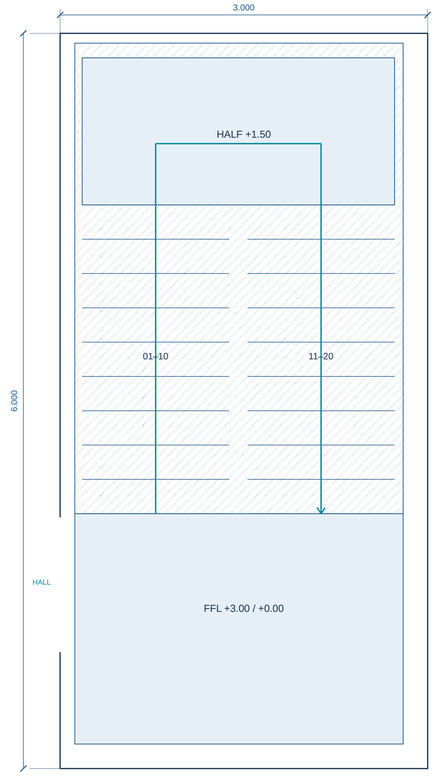

HALL AND DOORS

Hall x=4.50–6.00 = 1.50 clear. Lower exterior door only at z=8; upper exterior door only at z=0. Clear width 1.10. The opposite wall stays closed on each floor.

UPPER OPENING

Remove [6.12, 2.08, 2.68, 3.84] from upper slab in home-local x/z. Keep the top landing at z=5.92–7.80. Do not cut the whole 3 × 6 stair allocation out of the upper floor.

PRIVATE STAIR

ST-H: two 1.20 flights; 20 × 0.15 rises; 9 × 0.28 goings per half. Half landing 1.20. Upper and lower hall portals at z=6.50; both open onto solid full-level landing.

ROOM	LOWER CLEAR	UPPER CLEAR
Kitchen / bedroom 1	4.18 × 2.68	4.18 × 3.18
Living / bedroom 2	4.18 × 4.80	4.18 × 4.30
Hall	1.50 × 7.60	1.50 × 7.60
WC / bath	2.68 × 1.68	2.68 × 1.68
Stair allocation	3.00 × 6.00 gross	same; slab void differs

MIRROR AS ONE MODULE

For southern homes use world z = home.z + 8 - local z. This includes walls, windows, floors, floor hole, both flights and landing. Recalculate normals after baking the mirror.

EXACT NOSING POSITIONS

Home-local flight run z=3.40–5.92. Left flight x=6.18–7.38 rises north; right x=7.53–8.73 rises south. Half landing at +4.50. Top landing at +6.00. Stair tread/slab thickness 150 mm.

CLEARANCE

Leave at least 2.40 headroom; current repeated 3.00 storey / 0.20 slab gives 2.80 at landings. Place guards and rail posts outside the 1.20 clear flights. Test the actual capsule before adding art.

DIMENSIONED GAME-ENVIRONMENT DESIGN

For Blender blockout / proposed / not an as-built playable

Dimensions govern. All lengths in metres unless marked mm. Print A1 at 100%.

H2 MAISONETTE

SCALE 1:50 + 1:25 | PAPER 841 × 594 mm

MAP REV 01 + DETAIL ISSUE B01 / 18 OCTOBER 2026

DRAWN FROM METRIC DATA

build-spec.json + map.json


No networking / no runtime change

B301

B01 / ONSITE


ST-P / PLAN AT FULL LANDING

6 × 6 envelope / 1.50 clear flights / 200 mm outer shell

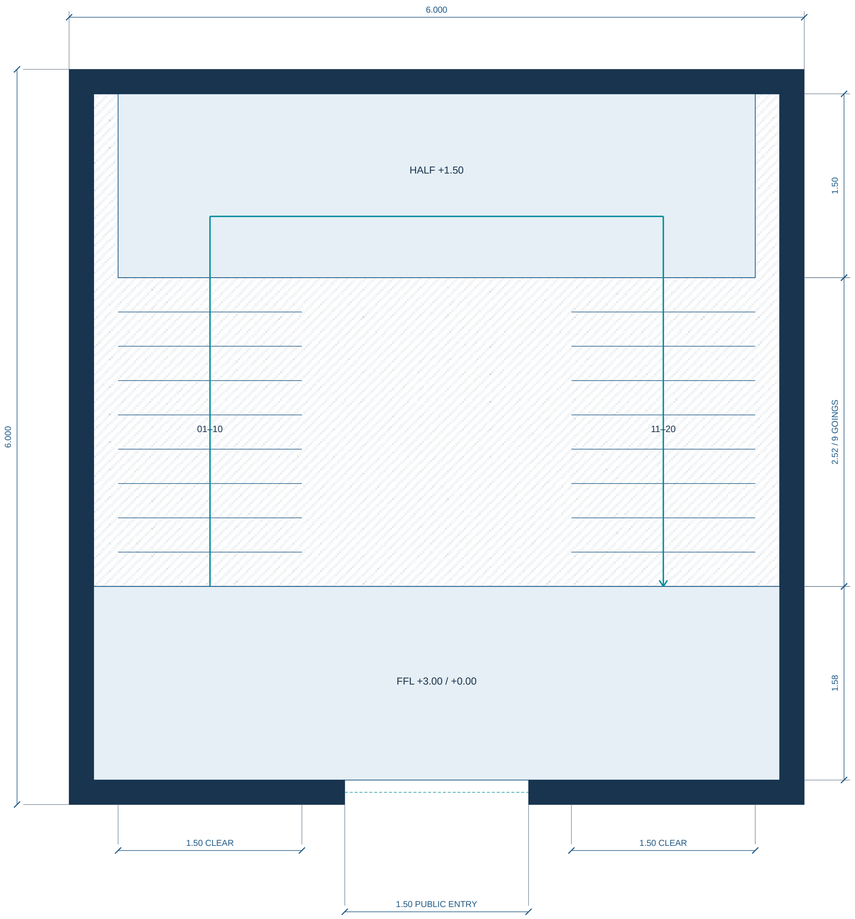

UNFOLDED WALKING LINE / 1:25

Section follows both flights; no vertical exaggeration.

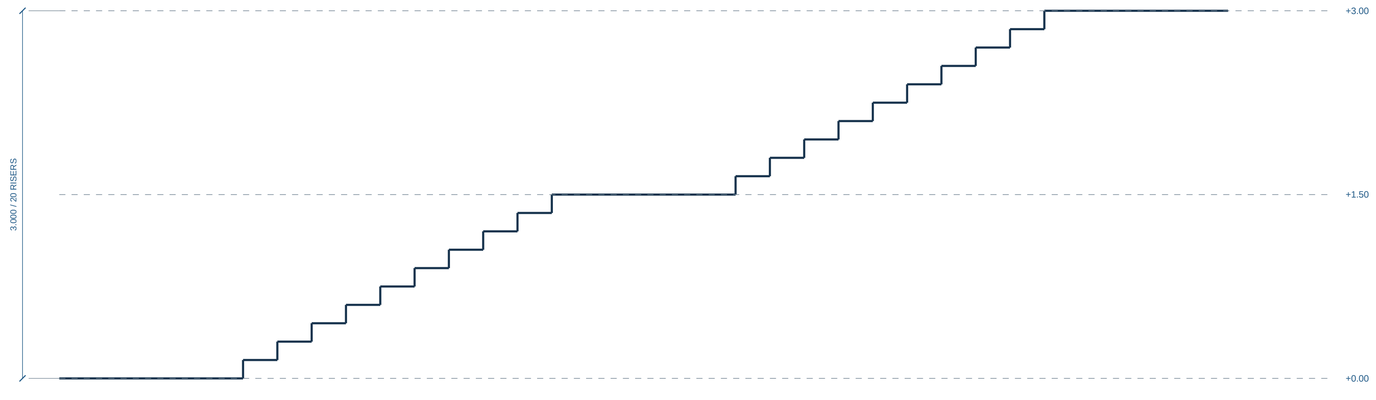

Each flight: 10 risers × 150 mm = 1.500 m rise; 9 treads × 280 mm = 2.520 m run. The tenth rise terminates at a landing. Do not add a tenth independent tread and then another riser at the landing.

PART	LOCAL RECTANGLE / X, Z, W, D	TOP
Half landing	0.40, 0.20, 5.20, 1.50	FFL +1.50
Full-level landing	0.20, 4.22, 5.60, 1.58	FFL +0 / +3
Floor void	0.20, 0.20, 5.60, 4.02	every served slab
Left clear flight	x 0.40–1.90 / z 1.70–4.22	rises north
Right clear flight	x 4.10–5.60 / z 1.70–4.22	rises south
Front portal	x 2.25–3.75 / z 5.80–6.00	2.40 clear head

LANDINGS / GUARDS

Guard flight voids at 1.20, handrail 1.00 above nosing line. Rail material must not reduce the specified clear width. Full-level landing connects to the external apron; no closed balustrade across that portal.


STACK AND CAP

Repeat at 3 m. Remove core volume from broad gallery floors and use this explicit slab opening/landing. Build no flight above the highest served level. Cap the top core at FFL +2.80; reserve 2.40 headroom below fittings.

1:25 AT A1 / METRES

0 — 2.5 — 5 m

LOCAL REAR / NORTH / 1:50

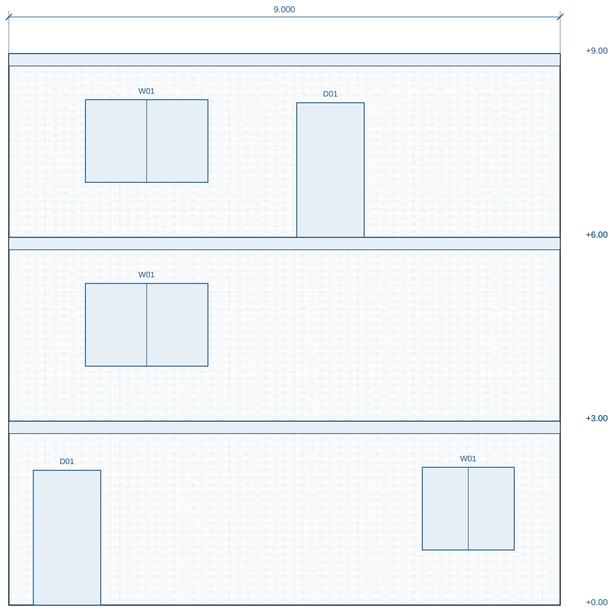


H1 0–3 / H2 lower 3–6 / H2 upper 6–9

1:50 AT A1 / METRES

0 2.5 5 m

LOCAL FRONT / SOUTH / 1:50

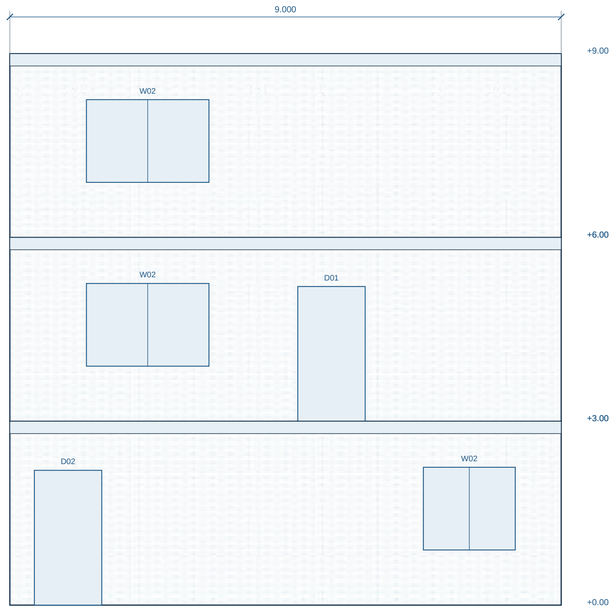

H1 0–3 / H2 lower 3–6 / H2 upper 6–9

1:50 AT A1 / METRES

0 2.5 5 m

READ AS MODULE ELEVATIONS

These are the home faces behind shared landings/concourse, not a fabricated full-building facade. B200/201 locates them inside the 36 × 18 block. Keep public circulation visible and open at its connections.


FACADE KIT

Use 3.00 × 3.00 bay logic, stock brick, 200 mm shell, concrete floor band and 80–120 mm recessed frames. Repeat with instancing, vary curtains/wear rather than geometry dimensions.

NO NEW ROUTES FROM WINDOWS

Home glass stays closed and non-traversable. Staging-facing service strips and roof screens remain opaque. Any new overlooking window needs a gameplay visibility review.

F01 / TYPICAL 3 M WINDOW BAY / 1:25

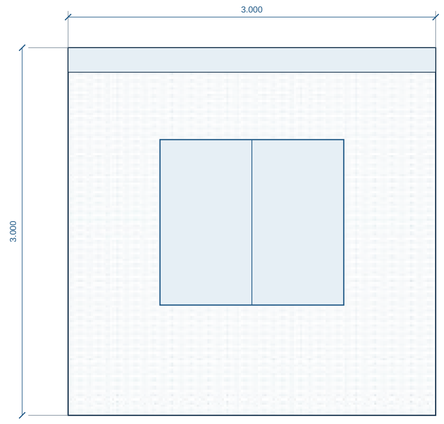


COMPONENT	DIMENSION / DATUM	MATERIAL
Exterior wall	0.20 / within footprint	M01 stock brick
Window W01 H1	1.50 × 1.35 / sill +0.90	M05 frame + closed glass
Window W01 H2	2.00 × 1.35 / sill +0.90	same shared material
Home doorway	1.10 × 2.20 clear	M05 / held open initially
Floor edge	0.20 deep below FFL	M02 concrete
Parapet / guard	1.20 above deck	M02 + M05
Sign / number plate	0.30 × 0.18 / centre +1.55	shared text/decal atlas

Frame recess, drip, sill and material joints belong to render geometry. Collision uses the simple wall aperture and closed glass plane. Do not let bevels, trims or dirt decals reduce clear doors, stairs or passage widths. Building lights are recreated in Three.js; Blender lamps are review-only.

A-A / ROWAN + S1 / LOOK EAST / 1:100

Section x=27 passes through the H1 hall, H2 rooms, rear landing, concourse and central stair well.

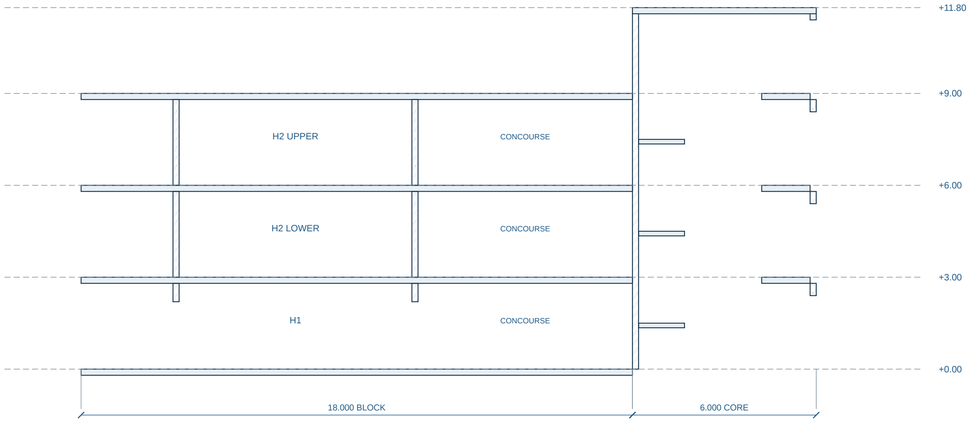

1:100 AT A1 / METRES



SECTION CUT DISCIPLINE

A-A is at map x=27, within the central well of S1. The cut shows half/full landings, not a fictitious straight flight through the well. Flights are dimensioned on B302.

CEILING / SLAB

Storey 3.00; slab 0.20 below FFL; clear room height 2.80. Public portal head 2.40. Stair treads/landing soffits must never intrude into the 2.40 minimum headroom envelope.

UNDERCROFT

B1 FFL -3.00. Ground slab underside -0.20. Clear 2.80 before services; services no lower than +2.40 relative to B1. Only the service union and exit cores are excavated in the model.

D01 / FLOOR EDGE + GUARD / 1:25



SLAB 200 mm BELOW FFL

Posts/trim outside walk polygon


D02 / OPENING AND THRESHOLD / 1:25

ELEMENT	REQUIRED CLEARANCE
Home door	1.10 wide × 2.20 high
Public portal	1.50 wide × 2.40 high
Home hall	1.50 clear between finish faces
Public stair flight	1.50 clear between rail faces
Private stair flight	1.20 clear between rail faces
Threshold	0.02 maximum; flush preferred
Collision plan	Match structural faces; exclude tiny trims

ONSITE / HERON REACH


Six shell interiors / explicit public doorways / four open court gates / furniture follows route clearance

18 × 9 SHOP TYPE

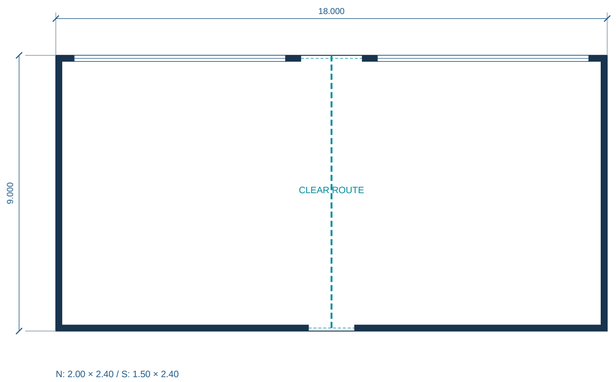


N: 2.00 × 2.40 / S: 1.50 × 2.40

6 × 18 SERVICE TYPE

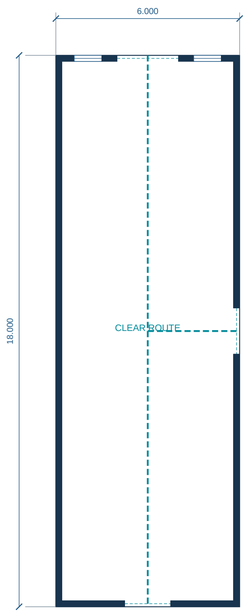

N: 2.00 × 2.40 / S: 1.50 × 2.40

THE CAGE / 30 × 20 / FOUR 4 M GATES

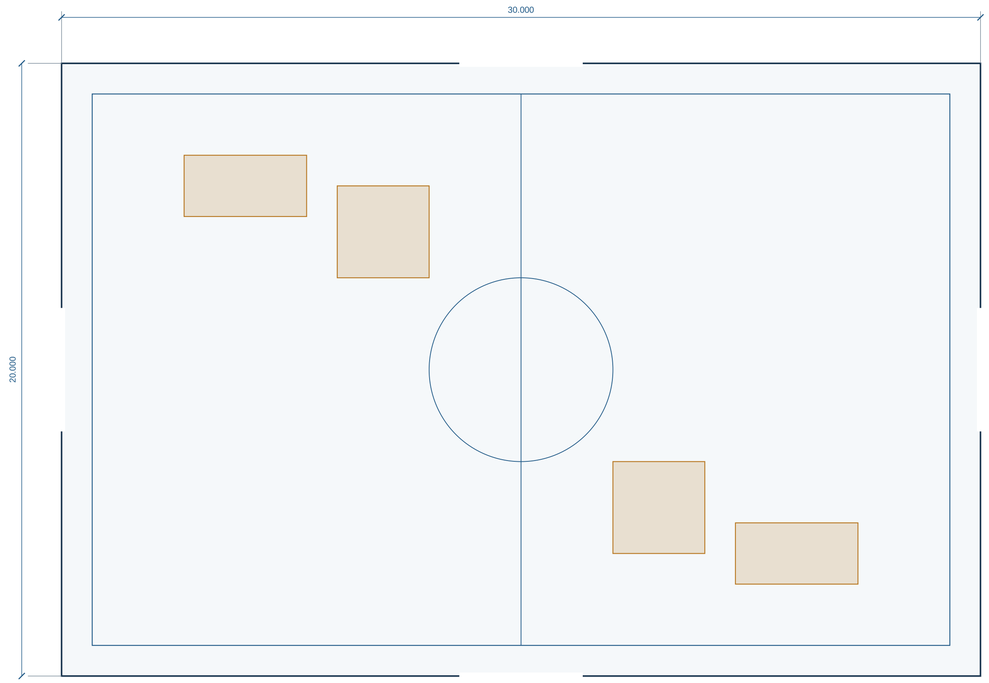

INSTANCE	ORIGIN X / Z	SIZE	SIDE DOOR
LAUNDERETTE	24 / 48	18 × 9	—
CYCLE WORKSHOP	24 / 63	18 × 9	—
THE CORNER	102 / 48	18 × 9	—
YOUTH ROOM	102 / 63	18 × 9	—
WASHHOUSE	60 / 87	6 × 18	E
ESTATE OFFICE	78 / 87	6 × 18	W

INTERIOR BUILD RULE

200 mm shell, 2.80 clear ceiling. Keep a 2.40 continuous route between portals; use display racks/appliances around the perimeter. Door leaves held open initially. Side service doors face Washhouse Square.

SHOPFRONT

N-side display glass: sill 0.60, head 2.20. Spans from x=0.60 to centre-1.50 and centre+1.50 to width-0.60. Fascia and shutters are render details; do not seal the scheduled front door.

COURT ASSEMBLY

Map origin (57,50). Fence 2.60 high; four 4.00 gates at side midpoints. Paint rectangle inset 1.00. Mesh is visually porous; define bullet/collision behaviour explicitly. No physics for painted lines.

USEFUL COVER

Low cover height 1.00; tall screens 2.10. Exact cover placements stay in map.json / cover-placements.csv. Dirty edges and nets are cosmetic; use measured box collision for rigid cover.

1:100 AT A1 / METRES

0 5 10 m

DIMENSIONED GAME-ENVIRONMENT DESIGN

For Blender blockout / proposed / not an as-built playable

Dimensions govern. All lengths in metres unless marked mm. Print A1 at 100%.

SHOPS AND COURT

SCALE 1:100 | PAPER 841 × 594 mm

MAP REV 01 + DETAIL ISSUE B01 / 18 OCTOBER 2026

DRAWN FROM METRIC DATA

build-spec.json + map.json


No networking / no runtime change

B500

B01 / ONSITE

ONSITE / HERON REACH

20 trees / 10 soil-grass zones / 7 wet patches / 20 fixture intentions / five dressing zones

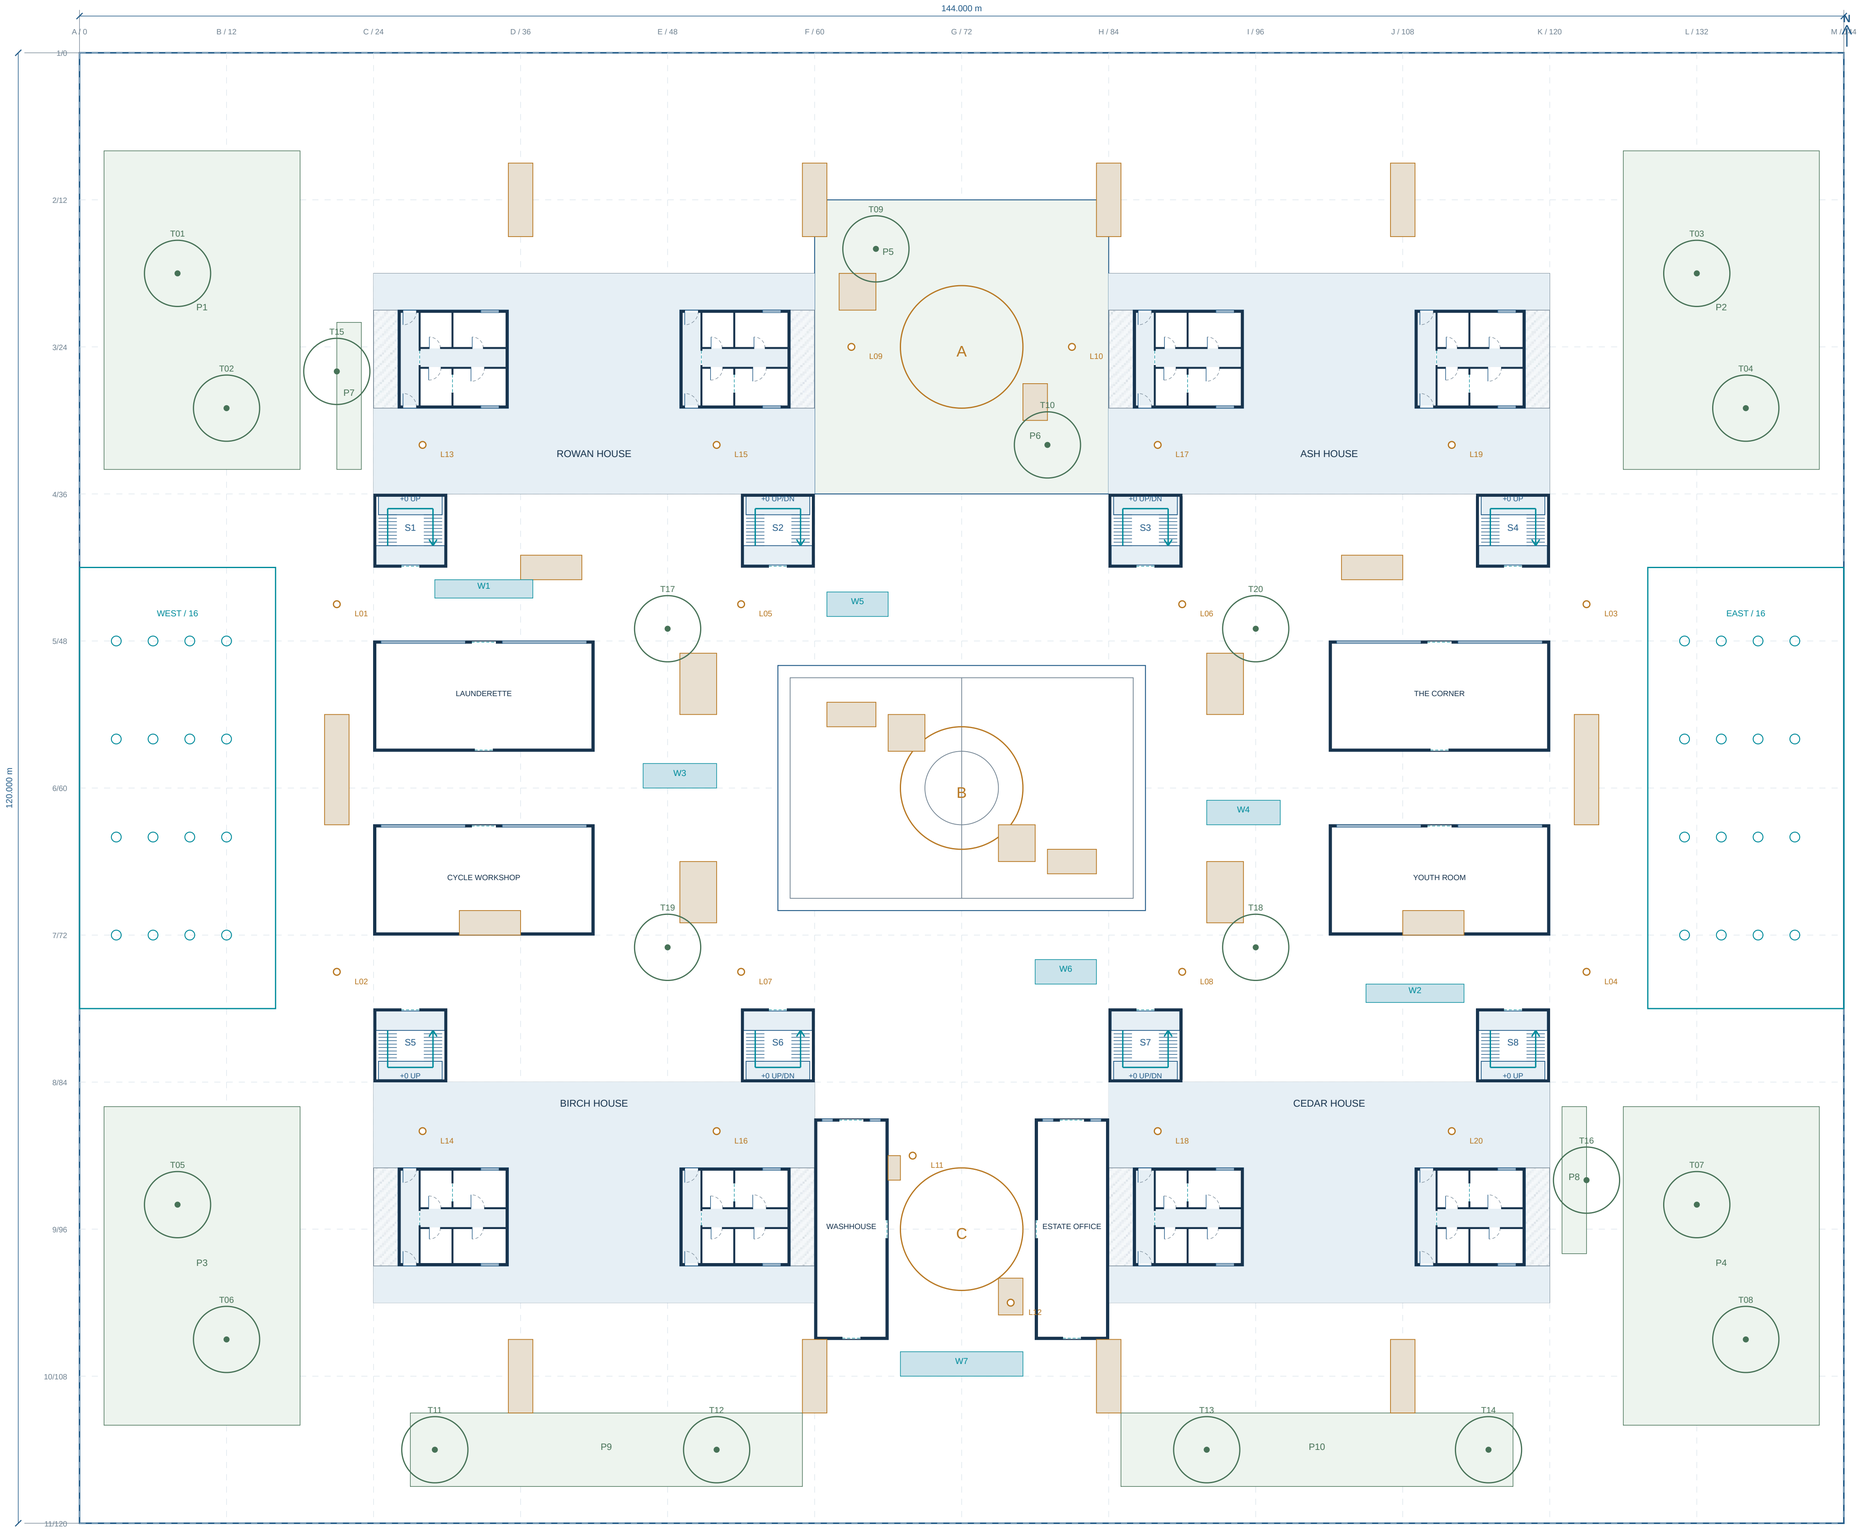

LONDON GROUND LAYERS

M03 asphalt to service lanes; M04 slabs to concourses. Dirt at drains/thresholds, moss on shaded concrete, leaves under trees, litter at shops and bin bays. Do not distribute grime uniformly.

TREE AND PLANTING CLEARANCE

Trunks use measured colliders. Canopies start 2.70 above ground. Shrubs at routes stay below 0.70. Keep final foliage outside stair entries and door sweeps; leaf cards never provide dependable ballistic cover.

LIGHTING DIRECTION

Cool blue-hour ambient; 2700 K door/shop/street fixture intent and 3000 K court fixtures. Warm thresholds reveal black clothing. Light positions/heights are in CSV; rebuild the lighting in Three.js.

WETNESS IS A MATERIAL LAYER

W1–W7 indicate shallow surface wetness. No extra collision. Use roughness variation and local puddle masks; preserve dry readable paths. Source texture packs are not all runtime-ready PBR.

DRESSING OWNERSHIP

Small paper/leaves/grass are render-only. Large bins, tree trunks and planters need explicit collision. Keep render, collision and navigation separate and use measured LOD/instancing budgets.

1:250 AT A1 / METRES

0 — 10 — 20 m

DIMENSIONED GAME-ENVIRONMENT DESIGN

For Blender blockout / proposed / not an as-built playable

Dimensions govern. All lengths in metres unless marked mm. Print A1 at 100%.

LANDSCAPE AND LIGHT

SCALE 1:250 | PAPER 841 × 594 mm

MAP REV 01 + DETAIL ISSUE B01 / 18 OCTOBER 2026

DRAWN FROM METRIC DATA

build-spec.json + map.json

No networking / no runtime change

B600

B01 / ONSITE

ONSITE / HERON REACH

Collection naming, pivots, materials and export contract / build the physical route before decoration

COLLECTION	CONTENT	EXPORT ROLE
00_DATUMS	Site bounds, grid, FFL markers, origin empties	guide only
10_GROUND / 11_UNDERCROFT	Union floors, explicit voids / tunnel shell	render and separate collision source
20_BLOCKS / 21_HOMES	Shared concourses; H1 and H2 placed modules	render chunks by block / storey
30_STAIRS / 31_GUARDS	ST-P and ST-H, mirrored with their instance	measured collision / floor links
40_SHOPS / 41_COURT	Door apertures, court fences and cover	render / rigid props collision
50_LANDSCAPE / 51_DECALS	Trees, grass, dirt, puddles, litter	render; trunks separately collidable
60_LIGHT_INTENT	Fixture emissive meshes + position empties	lights recreated in Three.js
90_COLLISION / 91_NAV_GUIDES	Simple solids / floor-aware portal labels	separate; not duplicate controllers

PIVOTS AND AXES

Use one Blender unit = one metre. Site pivot is world centre at (0,0,0). Module pivot is local minimum x/z at FFL. Apply transforms and recalculate normals after mirroring; keep scale +1.0. Bake the coordinate conversion once.


EXPORT CONTRACT

Export efficient render GLBs per spatial chunk. Preserve module/instance IDs as custom properties. Keep physical geometry and nav links in separate data. The existing WWB runtime uses one Rapier world and one actor movement owner.

DONT SHIP THE GUIDE AS FINAL ART

The companion .blend is exact blockout guidance with solid colours and labelled openings. It is separate from the old massing. Do not overwrite manual work or bundle the research clones. Donor assets still need their individual provenance.

D03 / GROUND EDGE / 1:25

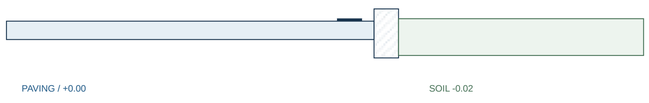

Drain slots, joints, moss and leaf litter follow edges. Kerbs stay outside primary walk polygons. Use flush transitions where the designed route crosses a change of material. Detail heights are render intent until capsule-tested.

ID	FAMILY	DETAIL / REUSE
M01	Stock brick	shared neutral base + local streak masks
M02	Concrete	gallery soffits, slab bands, nosings
M03	Asphalt	rain-dark base / isolated wetness
M04	Paving	slab joints and dirty drain edges
M05	Painted metal	railings, doors, frames, signs
M06	Soil / grass	beds and seams; alpha overdraw budget

ENVIRONMENT FINISH / DETAIL STACK / NTS

1. Structural silhouette and openings. 2. Recessed frames, parapets and soffits. 3. Shared PBR materials with consistent scale. 4. Dirt/wetness masks placed by water and use. 5. Instanced vegetation and rubbish. 6. Local lighting rebuilt and measured in Three.js.

ACCEPTANCE BEFORE ART

Walk every home exit and every stair both directions with actual capsules. Verify floor-aware bot routes at overlapping x/z, no double floors, correct roof closures, reliable headroom and no spawn sightlines. Then compare a camera view to the original London artwork.

ACCEPTANCE BEFORE CLAIMING 32 PLAYERS

Measure frame time, memory and load with populated actors on a real GPU. Route checks and these drawings do not prove game balance or server capacity. Networking is a separate later milestone.

DIMENSIONED GAME-ENVIRONMENT DESIGN

For Blender blockout / proposed / not an as-built playable

Dimensions govern. All lengths in metres unless marked mm. Print A1 at 100%.

BLENDER ASSEMBLY

SCALE 1:25 + NTS | PAPER 841 × 594 mm

MAP REV 01 + DETAIL ISSUE B01 / 18 OCTOBER 2026

DRAWN FROM METRIC DATA

build-spec.json + map.json

No networking / no runtime change

B700

B01 / ONSITE